





PERSPECTIVE

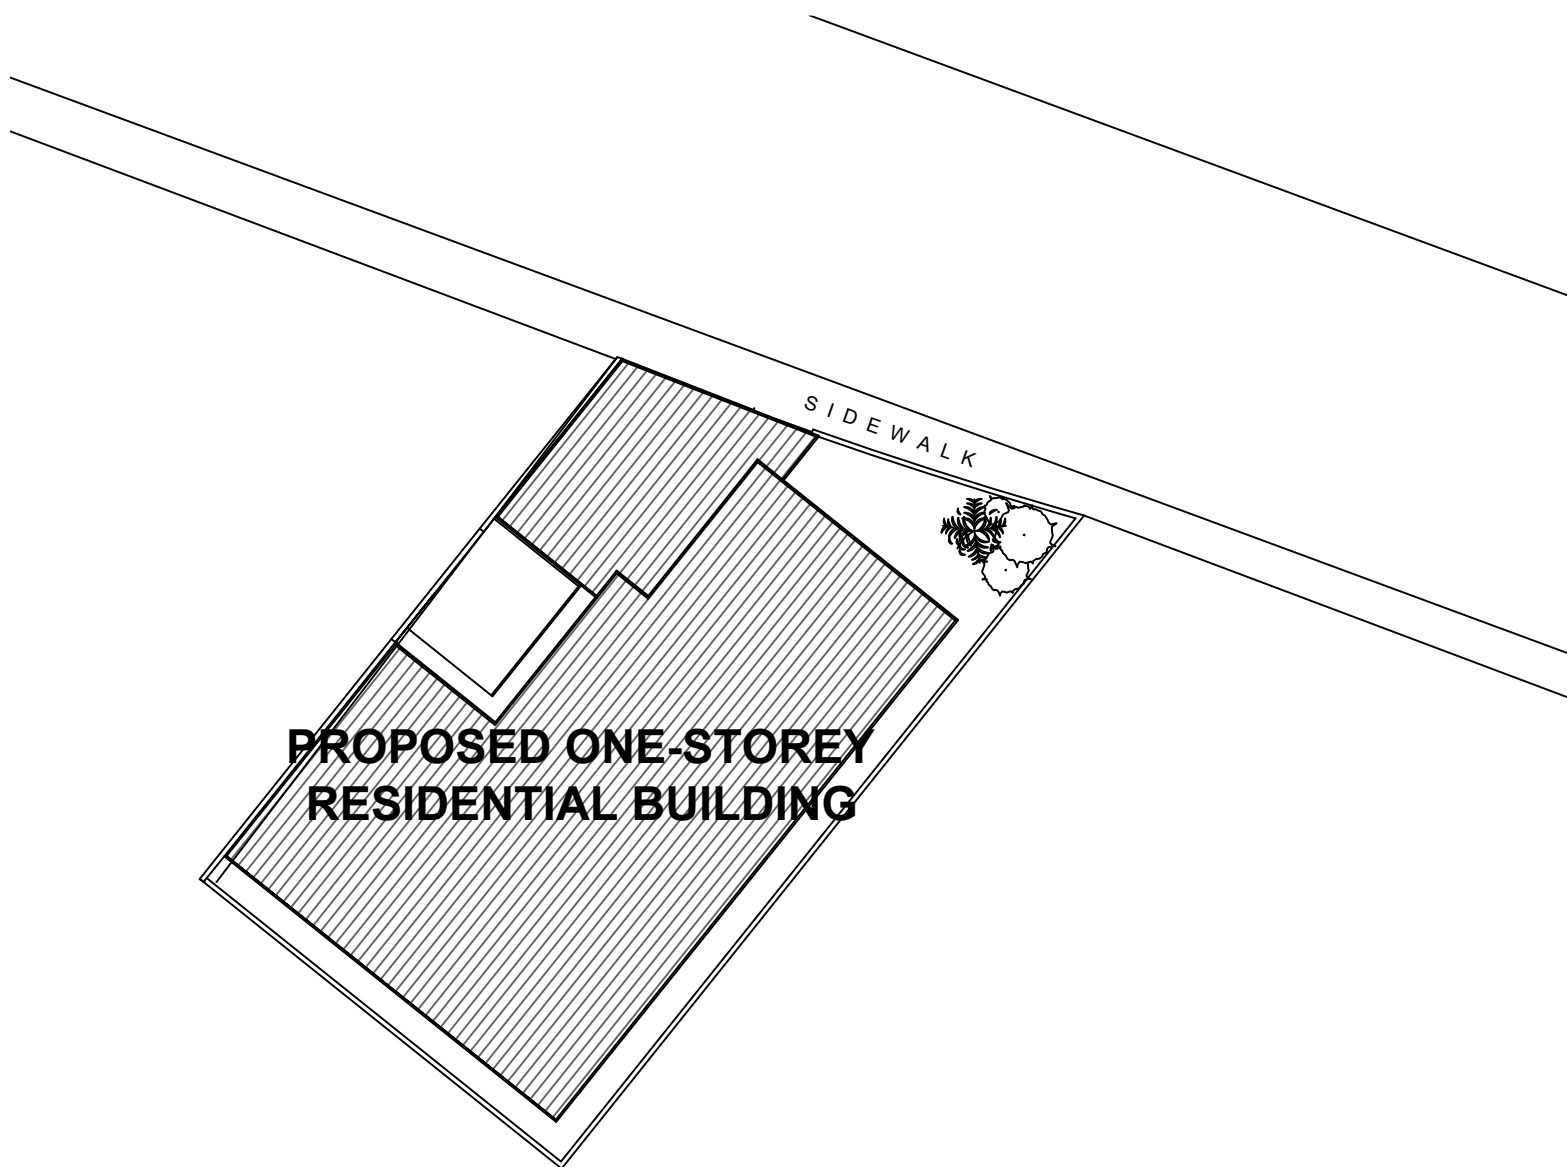

2 SITE DEVELOPMENT PLAN
CS 01 SCALE 1 : 150 M.

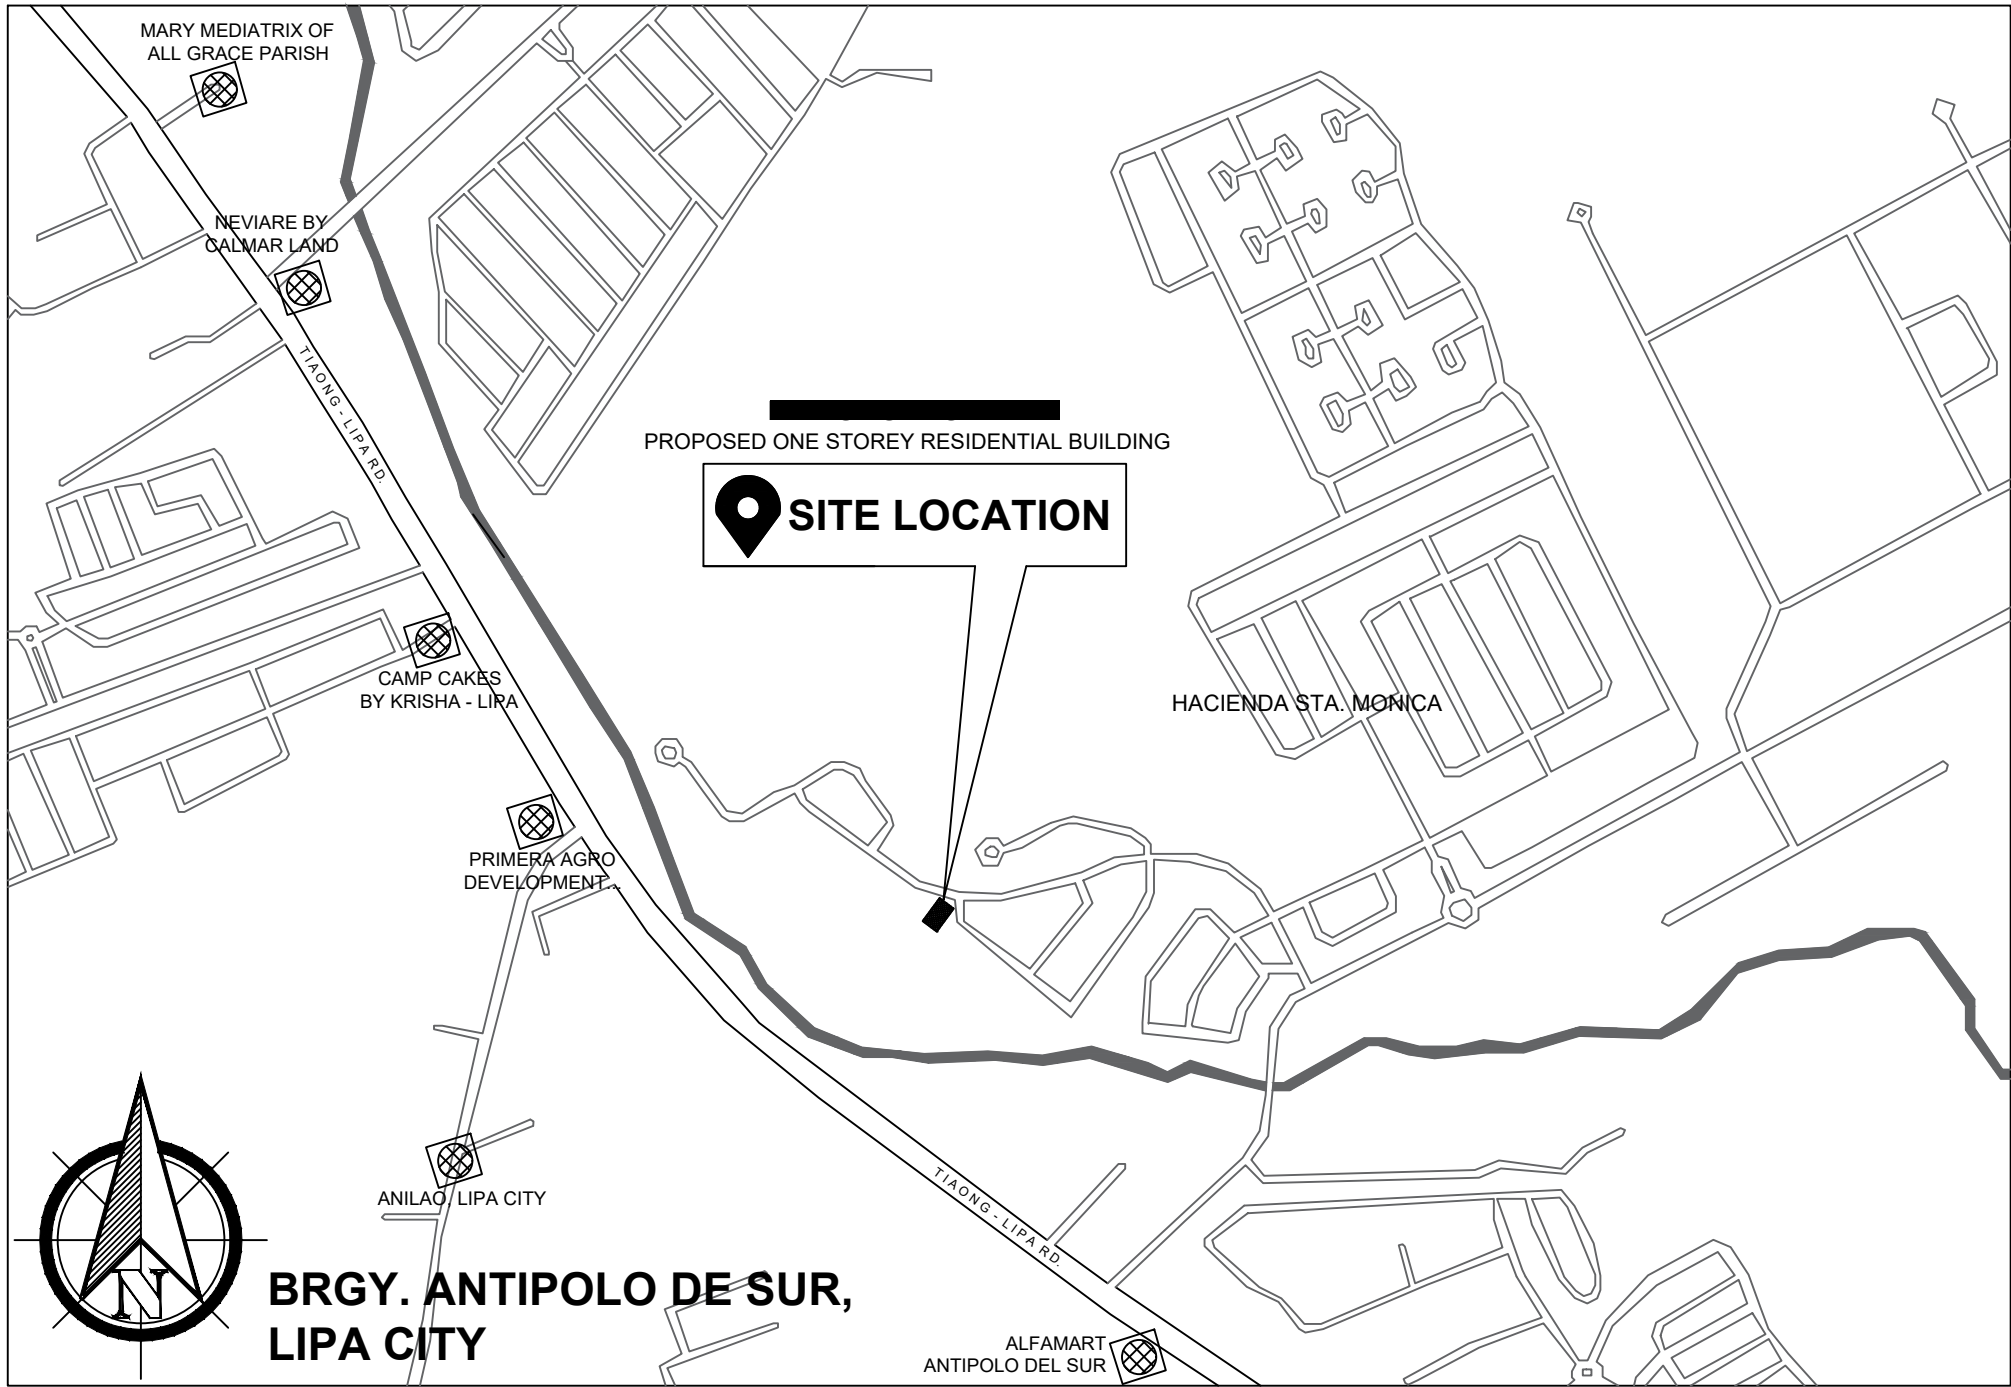

3 LOCATION MAP
CS 01 SCALE N T S

TABLE OF CONTENTS

- ARCHITECTURAL**
- A1 PERSPECTIVE
LOCATION MAP
 - A2 GROUND FLOOR PLAN
REFLECTED CEILING PLAN
 - A3 CROSS SECTION
LONGITUDINAL SECTION
SCHEDULE OF DOORS & WINDOWS
 - A4 FRONT ELEVATION
RIGHT SIDE ELEVATION
REAR ELEVATION
LEFT SIDE ELEVATION
 - A5 ROOF PLAN
CEILING DETAILS

- STRUCTURAL**
- S1 FOUNDATION PLAN
ROOF BEAM FRAMING PLAN
 - S2 ROOF FRAMING PLAN
ROOF FRAMING DETAILS
 - S3 COLUMN / FOOTING DETAILS
SLAB DETAIL
SLAB ON GRADE DETAIL
OPENING DETAILS
 - S4 SCHEDULE OF COLUMN
SCHEDULE OF BEAMS
NOTES & SPECIFICATIONS

- SANITARY**
- P1 PLUMBING LAYOUT
SANITARY LAYOUT
DETAILS
NOTES AND SPECIFICATIONS

- ELECTRICAL**
- E1 LIGHTING LAYOUT
POWER LAYOUT
LOAD SCHEDULE
NOTES AND SPECIFICATIONS

REPUBLIC OF THE PHILIPPINES
D P W H
OFFICE OF THE BUILDING OFFICIAL

DISTRICT / CITY / MUNICIPALITY

BUILDING OFFICIAL

LAND USE & ZONING

ARCHITECTURAL

STRUCTURAL

ELECTRICAL

SANITARY

MECHANICAL

FIRE CONTROL & SAFETY



ARCHITECT

ENGINEER

RA 9266 (ARCHITECTURE ACT OF 2004)
- SECTION 33

PROJECT / LOCATION

OWNER

DESIGNED:

No.

REVISIONS

DATE

SHEET CONTENT

SHEET No.

PRC No.:

IAPOA No.:

PTR No.:

PLACE:

DATE:

TIN:

PRC No.:

PTR No.:

PLACE:

DATE:

TIN:

DRAWING & SPECIFICATION DULY SIGNED, STAMPED OR
SEALED AS INSTRUMENT OF SERVICE ARE THE PROPERTY
AND DOCUMENTS OF THE ARCHITECT. WHETHER THE
OBJECT FOR WHICH THEY ARE MADE IS EXECUTED OR
NOT, IT SHALL BE UNLAWFUL FOR ANY PERSON WITHOUT
THE WRITTEN CONSENT OF THE ARCHITECT OR AUTHOR
OF THE SAID DOCUMENTS TO DUPLICATE FOR USE IN THE
REPETITION & FOR OTHER PROJECTS OR BUILDERS
WETHER EXECUTED PARTLY OR IN WHOLE.

PROPOSED ONE STOREY RESIDENTIAL BUILDING

[Redacted Owner Name]

DRAWN:

CHECKED:


DATE:

PERSPECTIVE
SITE DEVELOPMENT PLAN
LOCATION MAP


A-1

1

5

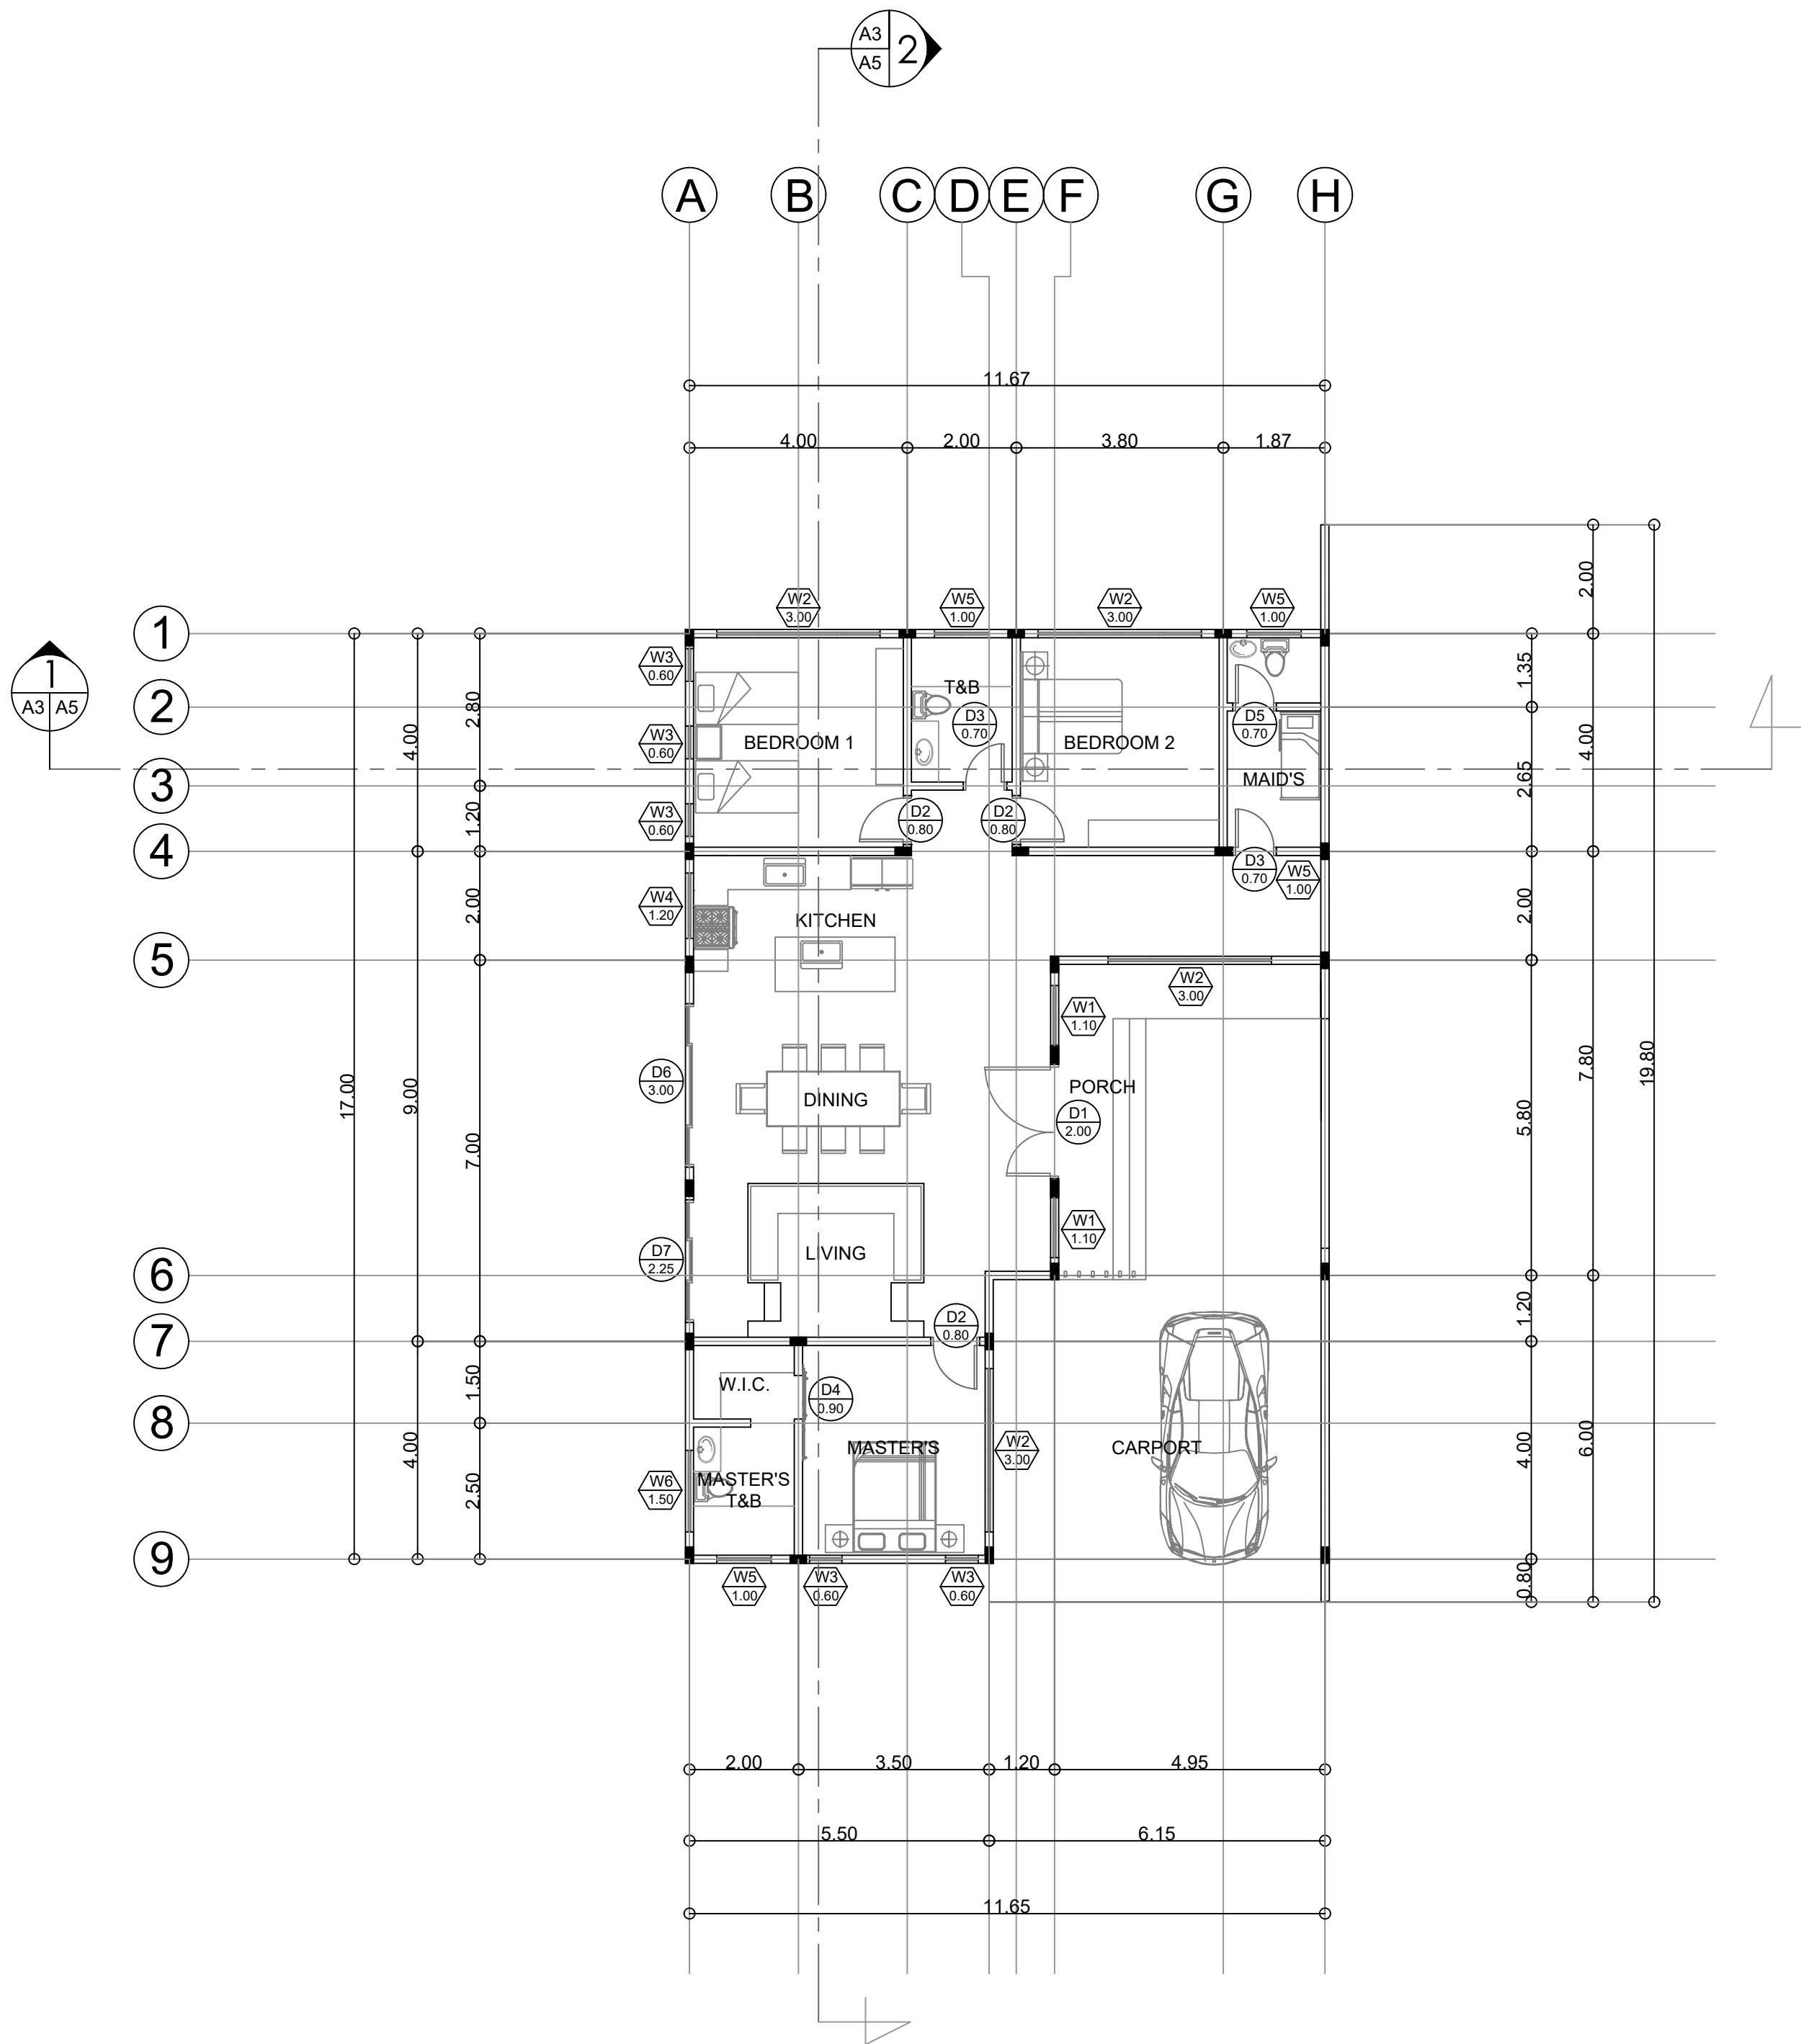

1 GROUND FLOOR PLAN
A2 A5 SCALE 1 : 100 M.

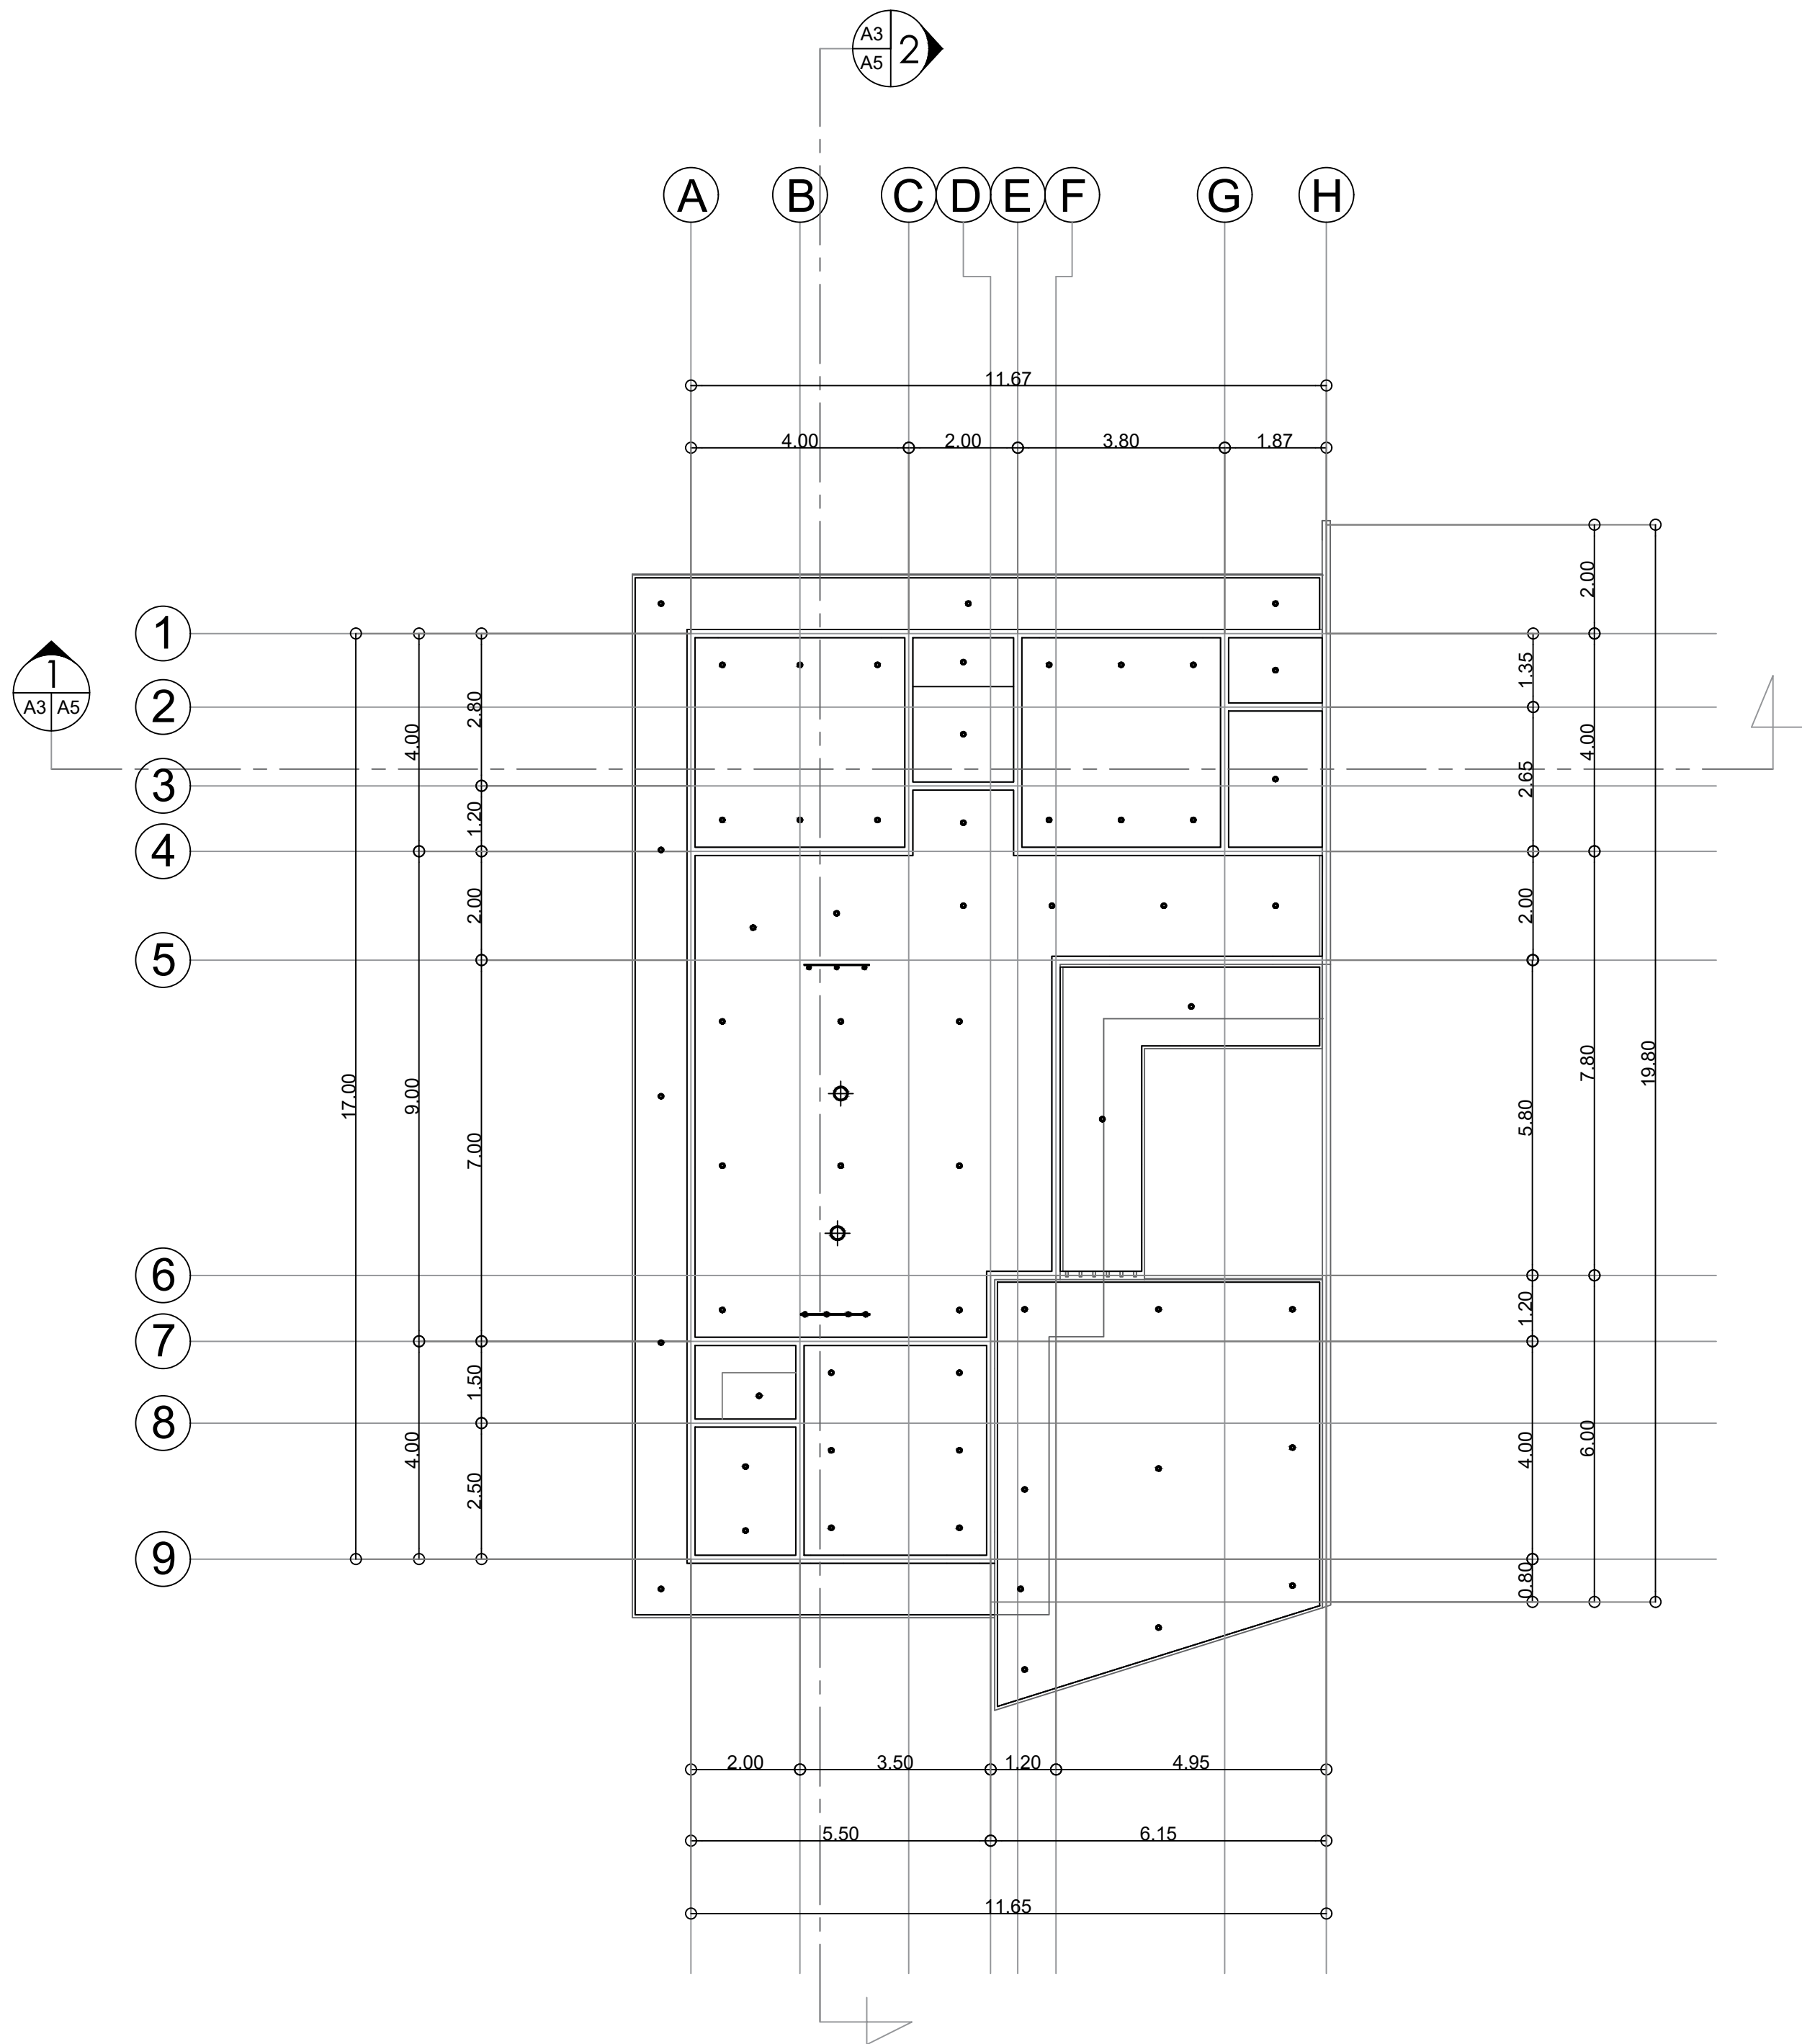

2 REFLECTED CEILING PLAN
A2 A5 SCALE 1 : 100 M.



ARCHITECT		ENGINEER	
PRC No.:		PRC No.:	
IAPOA No.:		PTR No.:	
PTR No.:		DATE:	
PLACE:		TIN:	

RA 9266 (ARCHITECTURE ACT OF 2004) - SECTION 33
DRAWING & SPECIFICATION DULY SIGNED, STAMPED OR SEALED AS INSTRUMENT OF SERVICE ARE THE PROPERTY AND DOCUMENTS OF THE ARCHITECT. WHETHER THE OBJECT FOR WHICH THEY ARE MADE IS EXECUTED OR NOT, IT SHALL BE UNLAWFUL FOR ANY PERSON WITHOUT THE WRITTEN CONSENT OF THE ARCHITECT OR AUTHOR OF THE SAID DOCUMENTS TO DUPLICATE FOR USE IN THE REPETITION & FOR OTHER PROJECTS OR BUILDERS WHETHER EXECUTED PARTLY OR IN WHOLE.


PROJECT / LOCATION
PROPOSED ONE STOREY RESIDENTIAL BUILDING

OWNER


DESIGNED:	No.	REVISIONS	DATE

SHEET CONTENT
GROUND FLOOR PLAN REFLECTED CEILING PLAN


SHEET No.	
A-2	
2	5

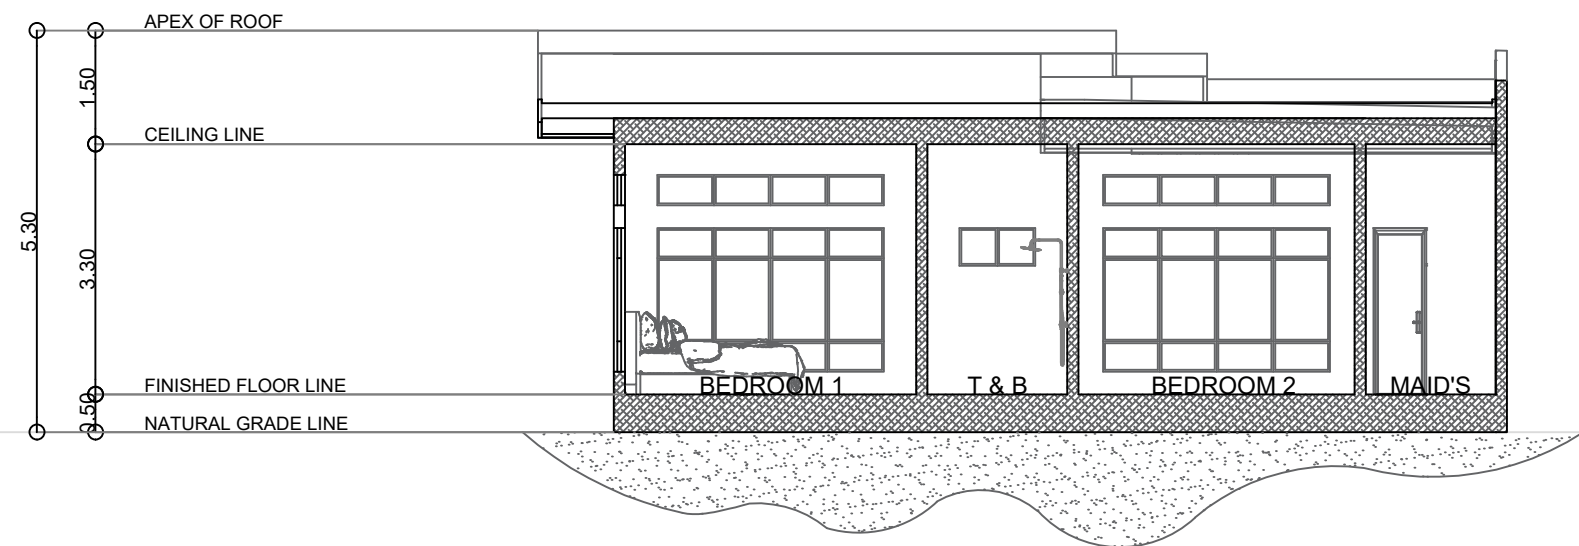

1 CROSS SECTION
A3 A5 SCALE 1 : 100 M.

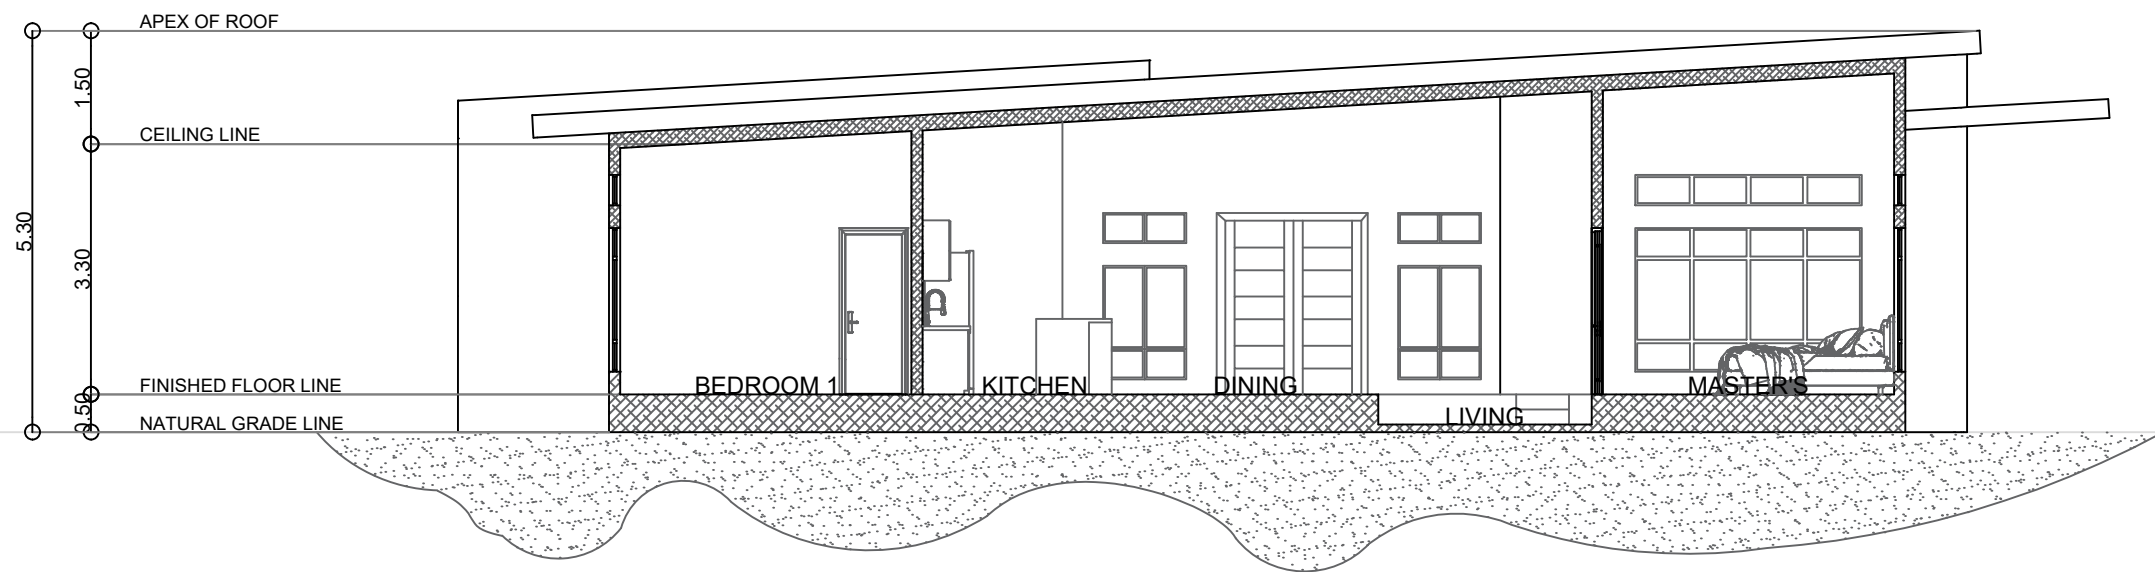

2 LONGITUDINAL SECTION
A3 A5 SCALE 1 : 100 M.

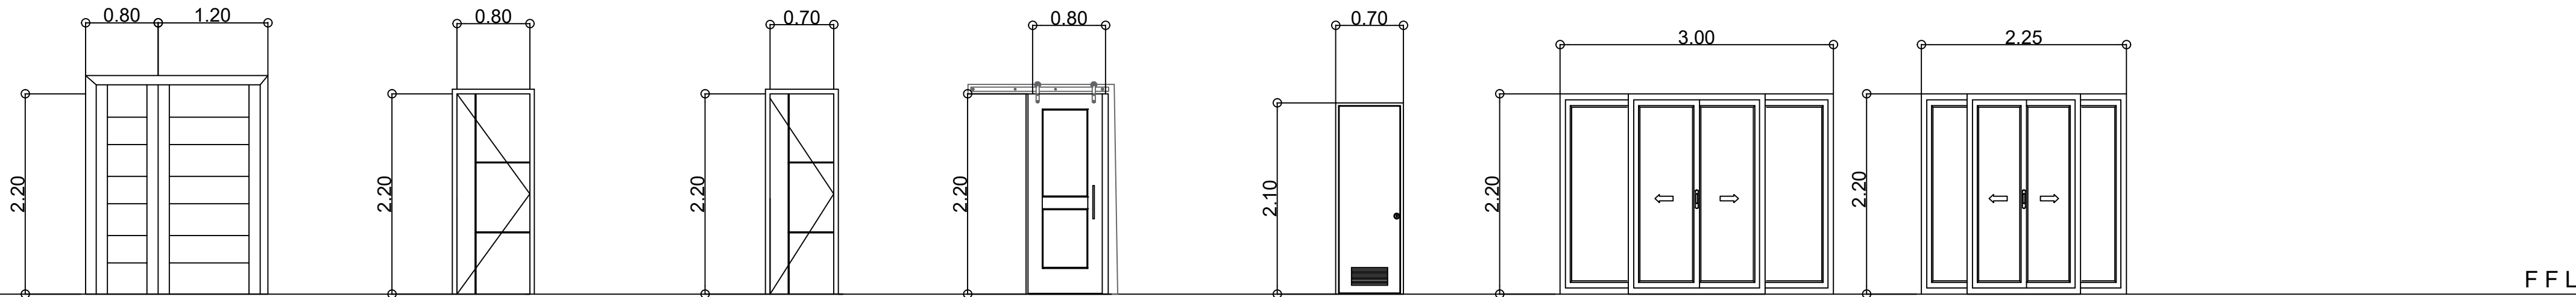

D1	SOLID PANEL DOOR WITH 2" X 4" STEEL DOOR JAMB
DESCRIPTION	
QUANTITY	MAKE 1 SET
LOCATION	PORCH

D2	SOLID PANEL DOOR WITH 2" X 4" STEEL DOOR JAMB
DESCRIPTION	
QUANTITY	MAKE 3 SETS
LOCATION	MASTERS, BEDROOM 1&2


D3	SOLID PANEL DOOR WITH 2" X 4" STEEL DOOR JAMB
DESCRIPTION	
QUANTITY	MAKE 2 SETS
LOCATION	T & B, MAID'S

D4	SOLID PANEL SLIDING DOOR
DESCRIPTION	
QUANTITY	MAKE 1 SET
LOCATION	MASTERS TAB

D5	PVC FLUSH DOOR
DESCRIPTION	
QUANTITY	MAKE 1 SET
LOCATION	BEDROOM, KITCHEN

D6	ALUMINUM-FRAMED SLIDING DOOR
DESCRIPTION	
QUANTITY	MAKE 1 SET
LOCATION	DINING AREA

D7	ALUMINUM-FRAMED SLIDING DOOR
DESCRIPTION	
QUANTITY	MAKE 1 SET
LOCATION	LIVING AREA

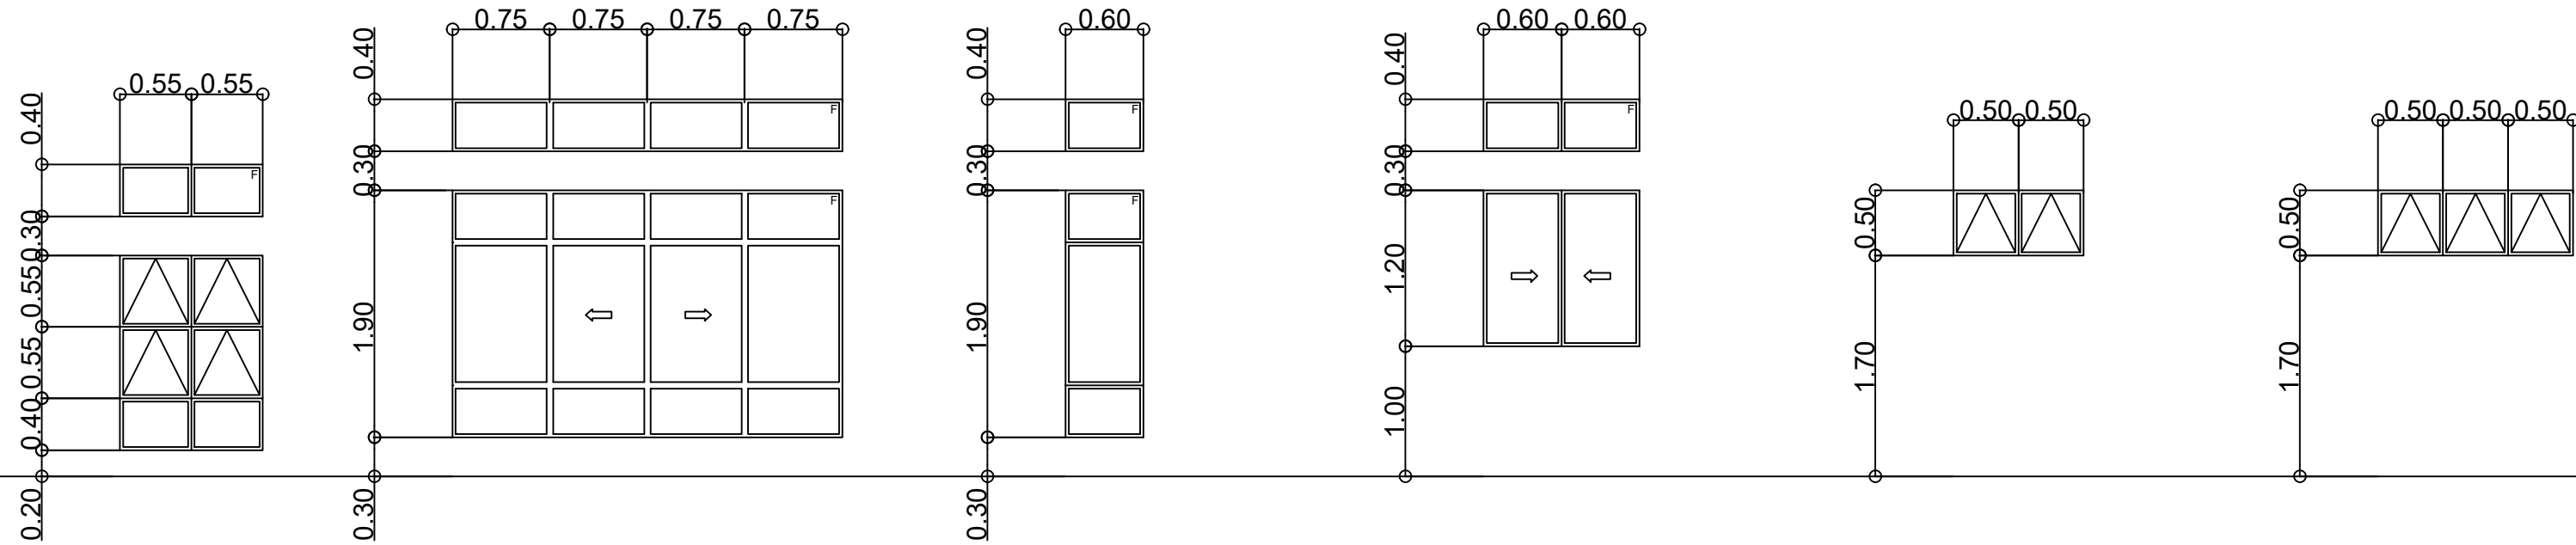

W1	ALUMINUM-FRAMED AWNING WINDOW
DESCRIPTION	
QUANTITY	MAKE 2 SETS
LOCATION	PORCH

W2	ALUMINUM-FRAMED SLIDING WINDOW
DESCRIPTION	
QUANTITY	MAKE 4 SETS
LOCATION	PORCH, MASTERS, BEDROOM

W3	ALUMINUM-FRAMED FIXED WINDOW
DESCRIPTION	
QUANTITY	MAKE 5 SETS
LOCATION	BEDROOM, MASTERS

W4	ALUMINUM-FRAMED SLIDING WINDOW
DESCRIPTION	
QUANTITY	MAKE 1 SET
LOCATION	KITCHEN


W5	ALUMINUM-FRAMED AWNING WINDOW
DESCRIPTION	
QUANTITY	MAKE 4 SETS
LOCATION	T & B, MASTERS TAB, MAID'S

W6	ALUMINUM-FRAMED WINDOW
DESCRIPTION	
QUANTITY	MAKE 1 SET
LOCATION	MASTERS TAB


3 SCHEDULE OF DOORS & WINDOWS
A3 A5 SCALE 1 : 50 M.




ARCHITECT	ENGINEER	RA 9266 (ARCHITECTURE ACT OF 2004) - SECTION 33	PROJECT / LOCATION	OWNER	DESIGNED:	No.	REVISIONS	DATE	SHEET CONTENT	SHEET No.
PRC No.: IAPOA No.: PTR No.: PLACE:	PRC No.: DATE: PLACE:	DRAWINGS & SPECIFICATION DULY SIGNED, STAMPED OR SEALED AS INSTRUMENT OF SERVICE ARE THE PROPERTY AND DOCUMENTS OF THE ARCHITECT. WHETHER THE OBJECT FOR WHICH THEY ARE MADE IS EXECUTED OR NOT, IT SHALL BE UNLAWFUL FOR ANY PERSON WITHOUT THE WRITTEN CONSENT OF THE ARCHITECT OR AUTHOR OF THE SAID DOCUMENTS TO DUPLICATE FOR USE IN THE REPETITION & FOR OTHER PROJECTS OR BUILDERS WETHER EXECUTED PARTLY OR IN WHOLE.	PROPOSED ONE STOREY RESIDENTIAL BUILDING		DRAWN: CHECKED: DATE:				CROSS SECTION LONGITUDINAL SECTION DOORS & WINDOWS SCHEDULE	A-3 3 5

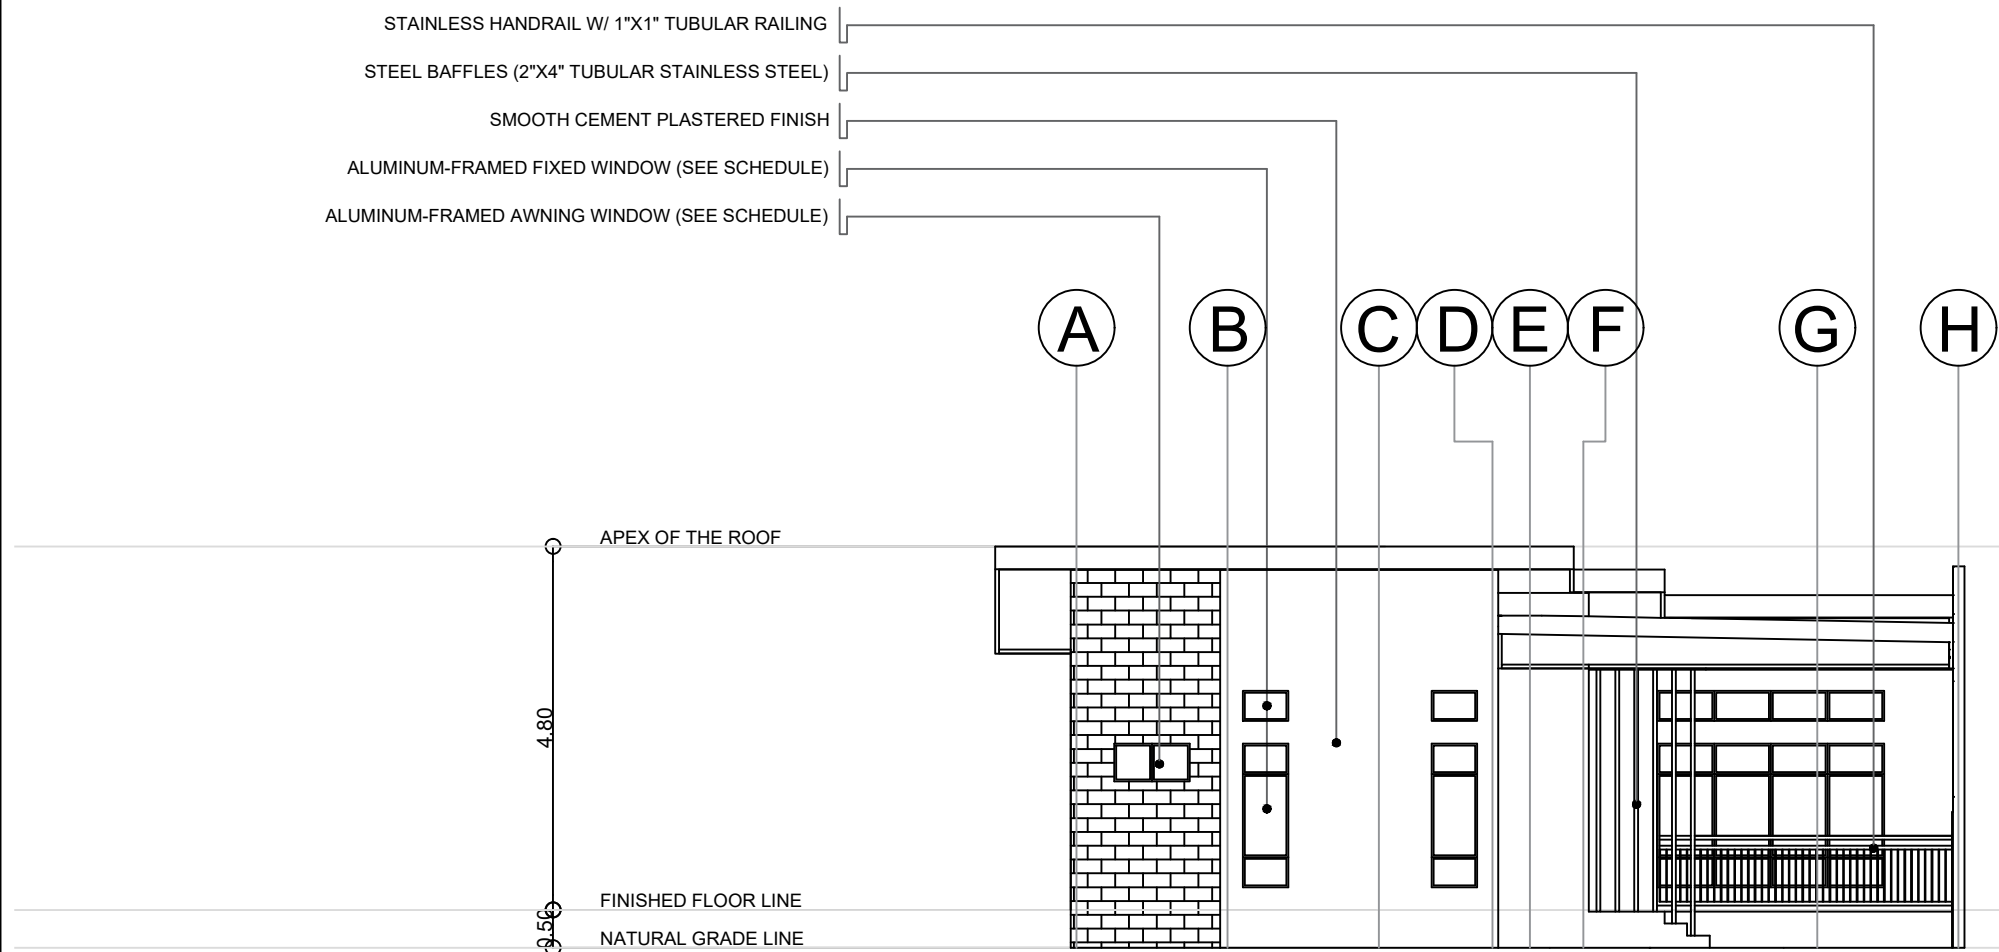


1 FRONT ELEVATION
A4 A5 SCALE 1 : 100 M.

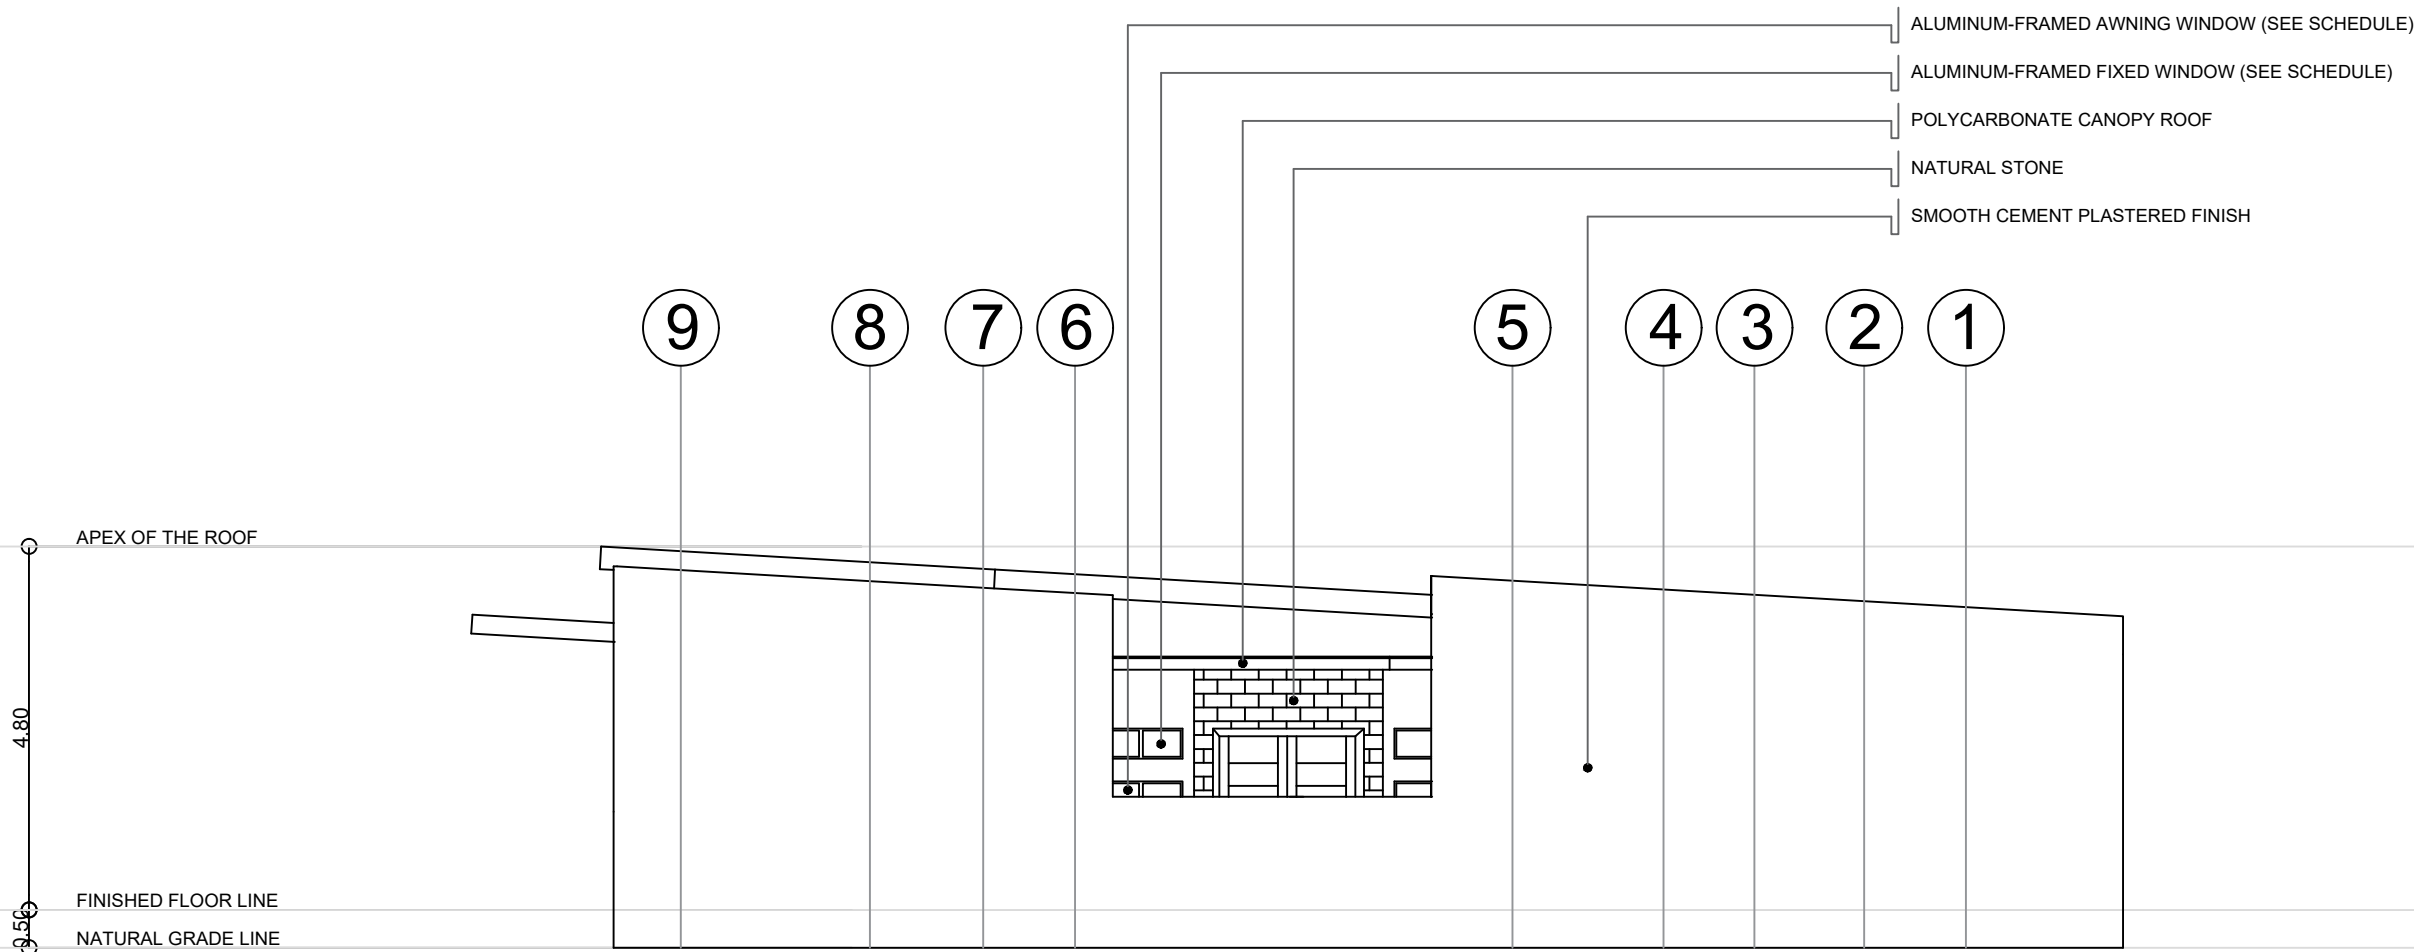

2 RIGHT SIDE ELEVATION
A4 A5 SCALE 1 : 100 M.

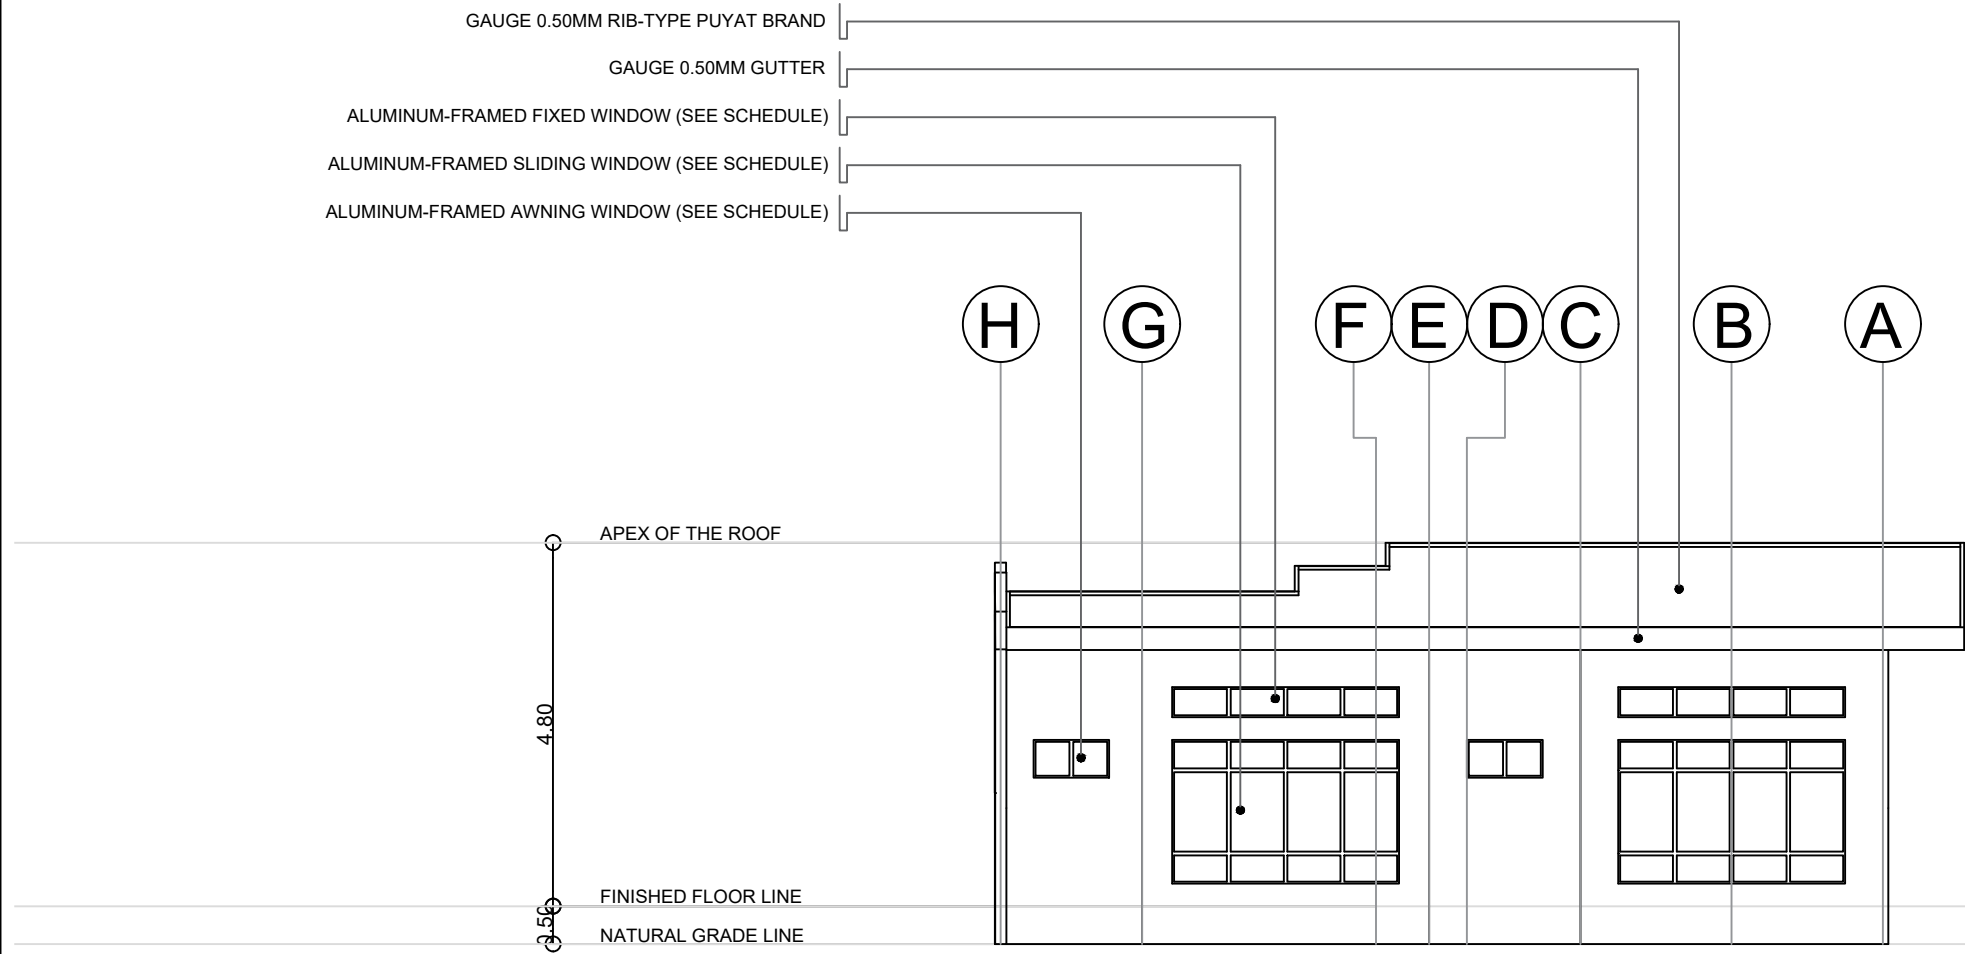

3 REAR ELEVATION
A4 A5 SCALE 1 : 100 M.

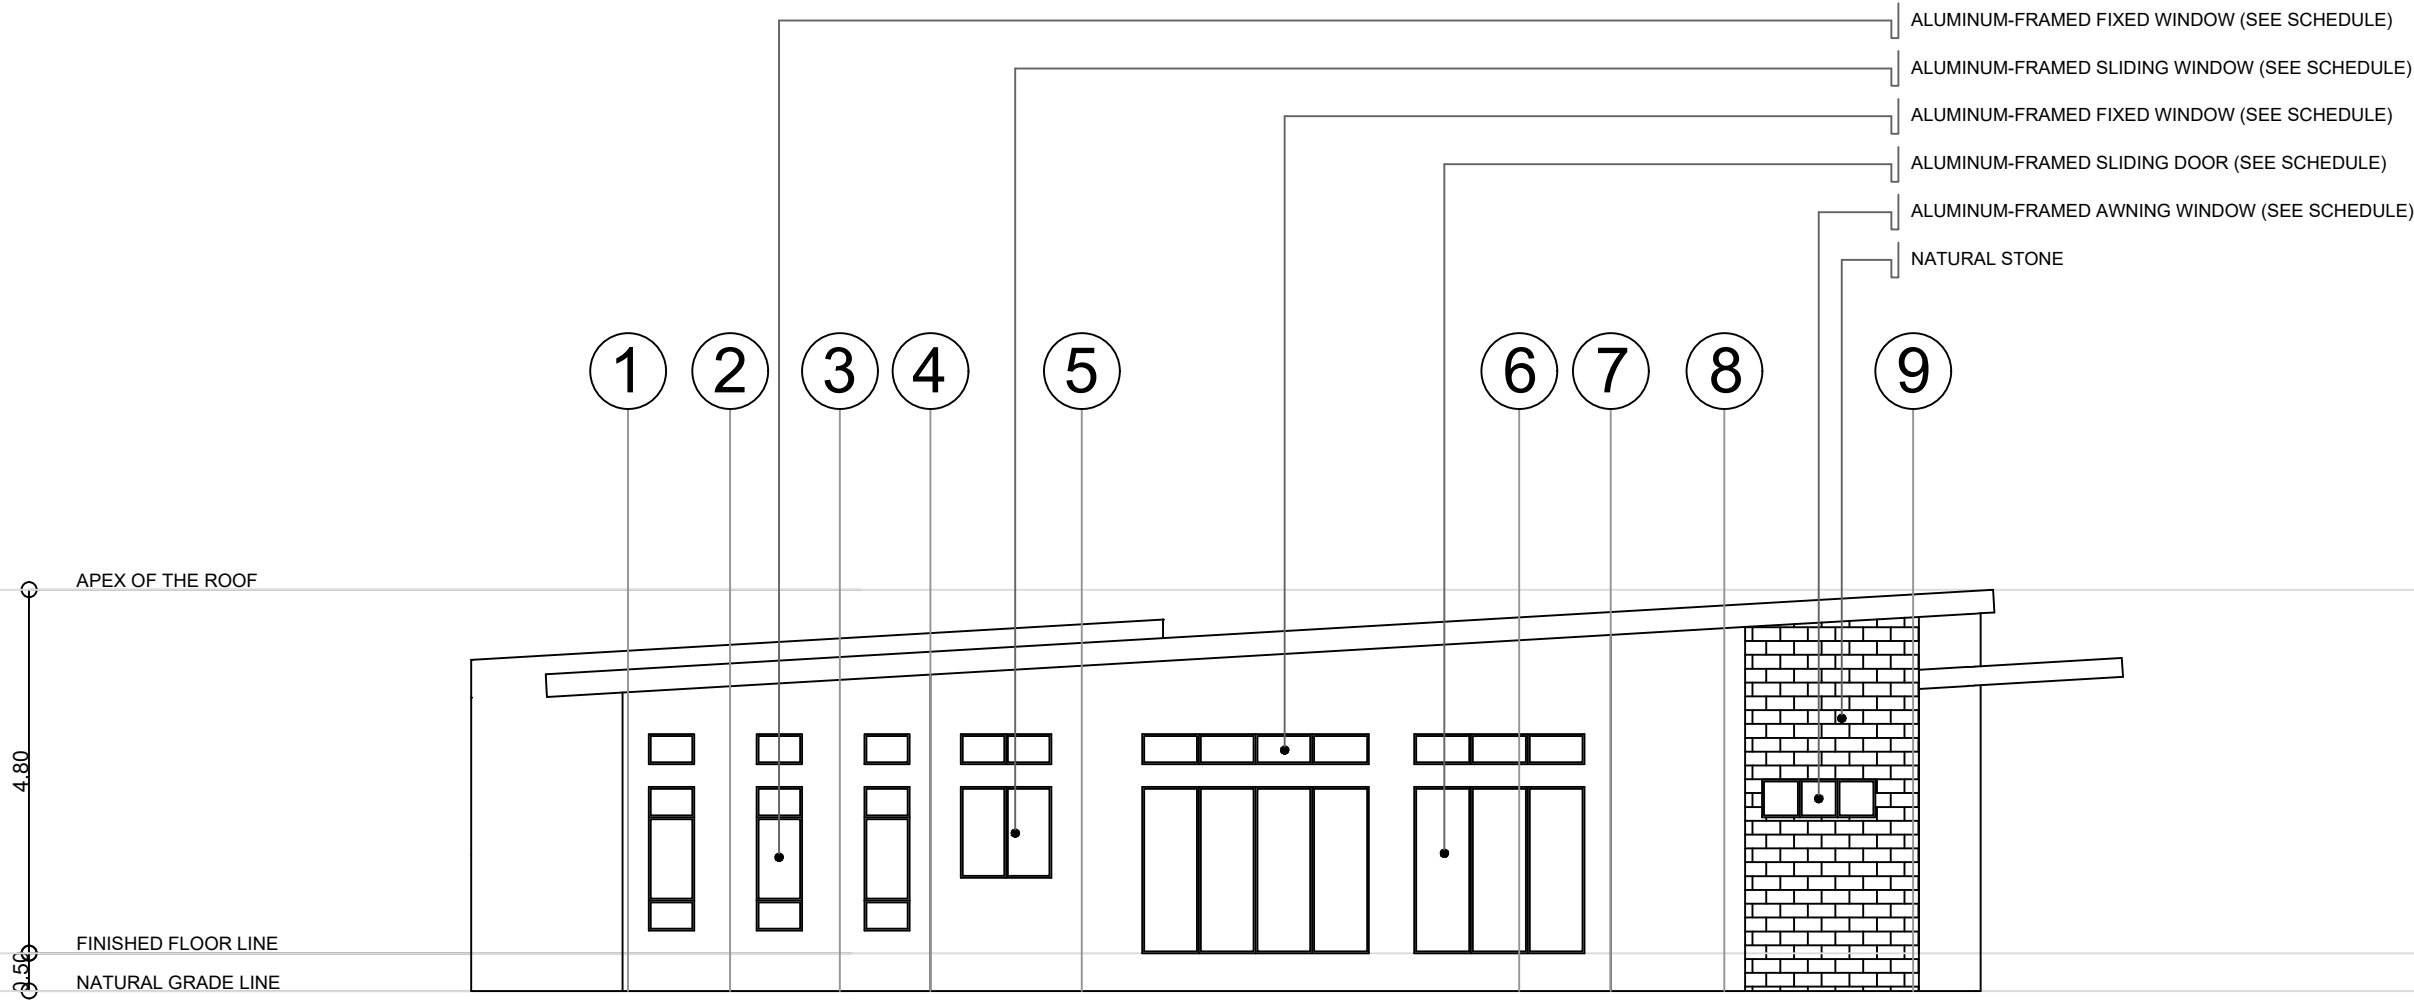

4 LEFT SIDE ELEVATION
A4 A5 SCALE 1 : 100 M.



ARCHITECT		ENGINEER	
PRC No.:		PRC No.:	
IAPOA No.:		PTR No.:	
DATE:		DATE:	
PLACE:		PLACE:	
TIN:		TIN:	

RA 9266 (ARCHITECTURE ACT OF 2004)
- SECTION 33


DRAWINGS & SPECIFICATION DULY SIGNED, STAMPED OR SEALED AS INSTRUMENT OF SERVICE ARE THE PROPERTY AND DOCUMENTS OF THE ARCHITECT. WHETHER THE OBJECT FOR WHICH THEY ARE MADE IS EXECUTED OR NOT, IT SHALL BE UNLAWFUL FOR ANY PERSON WITHOUT THE WRITTEN CONSENT OF THE ARCHITECT OR AUTHOR OF THE SAID DOCUMENTS TO DUPLICATE FOR USE IN THE REPETITION & FOR OTHER PROJECTS OR BUILDERS WETHER EXECUTED PARTLY OR IN WHOLE.


PROJECT / LOCATION
PROPOSED ONE STOREY RESIDENTIAL BUILDING


OWNER

DESIGNED:	No.	REVISIONS	DATE

SHEET CONTENT		SHEET No.	
ELEVATIONS		A-4	
4	5		

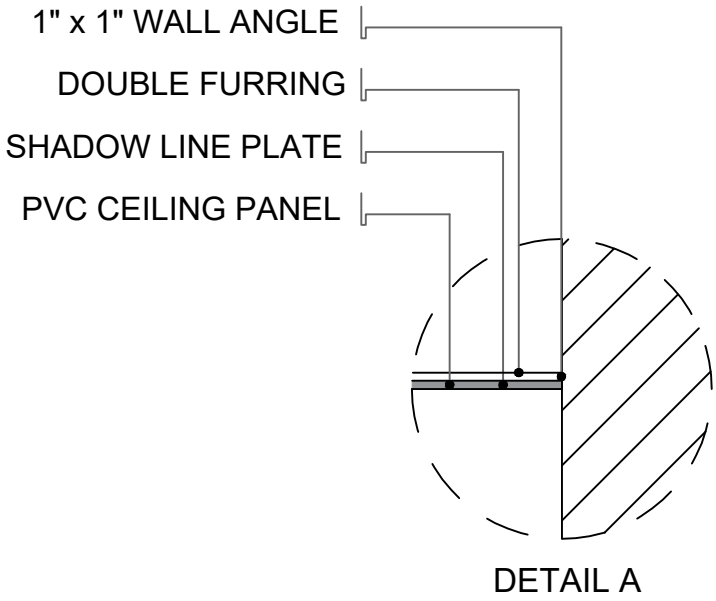

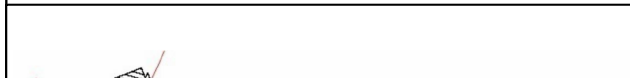 homeaccnt ARCHITECTURE • DESIGN • BUILDERS SALVADOR M. DE GRACIA CALUMPANG EAST, SAN LUIS, BATANGAS 09873447115	ARCHITECT		ENGINEER		RA 9266 (ARCHITECTURE ACT OF 2004) - SECTION 33		PROJECT / LOCATION		OWNER		DESIGNED:		No.	REVISIONS		DATE	SHEET CONTENT		SHEET No.	
					DRAWING & SPECIFICATION DULY SIGNED, STAMPED OR SEALED AS INSTRUMENT OF SERVICE ARE THE PROPERTY AND DOCUMENTS OF THE ARCHITECT. WHETHER THE OBJECT FOR WHICH THEY ARE MADE IS EXECUTED OR NOT, IT SHALL BE UNLAWFUL FOR ANY PERSON WITHOUT THE WRITTEN CONSENT OF THE ARCHITECT OR AUTHOR OF THE SAID DOCUMENTS TO DUPLICATE FOR USE IN THE REPETITION & FOR OTHER PROJECTS OR BUILDERS WHETHER EXECUTED PARTLY OR IN WHOLE.		PROPOSED ONE STOREY RESIDENTIAL BUILDING				DRAWN:					ROOF PLAN CEILING DETAILS		A-5		
	PRC No.:		PRC No.:								CHECKED:									
	IAPQA No.:																			
	PTR No.:		PTR No.:								DATE:									
PLACE:		DATE:		PLACE:		TIN:		DATE:								5	5			

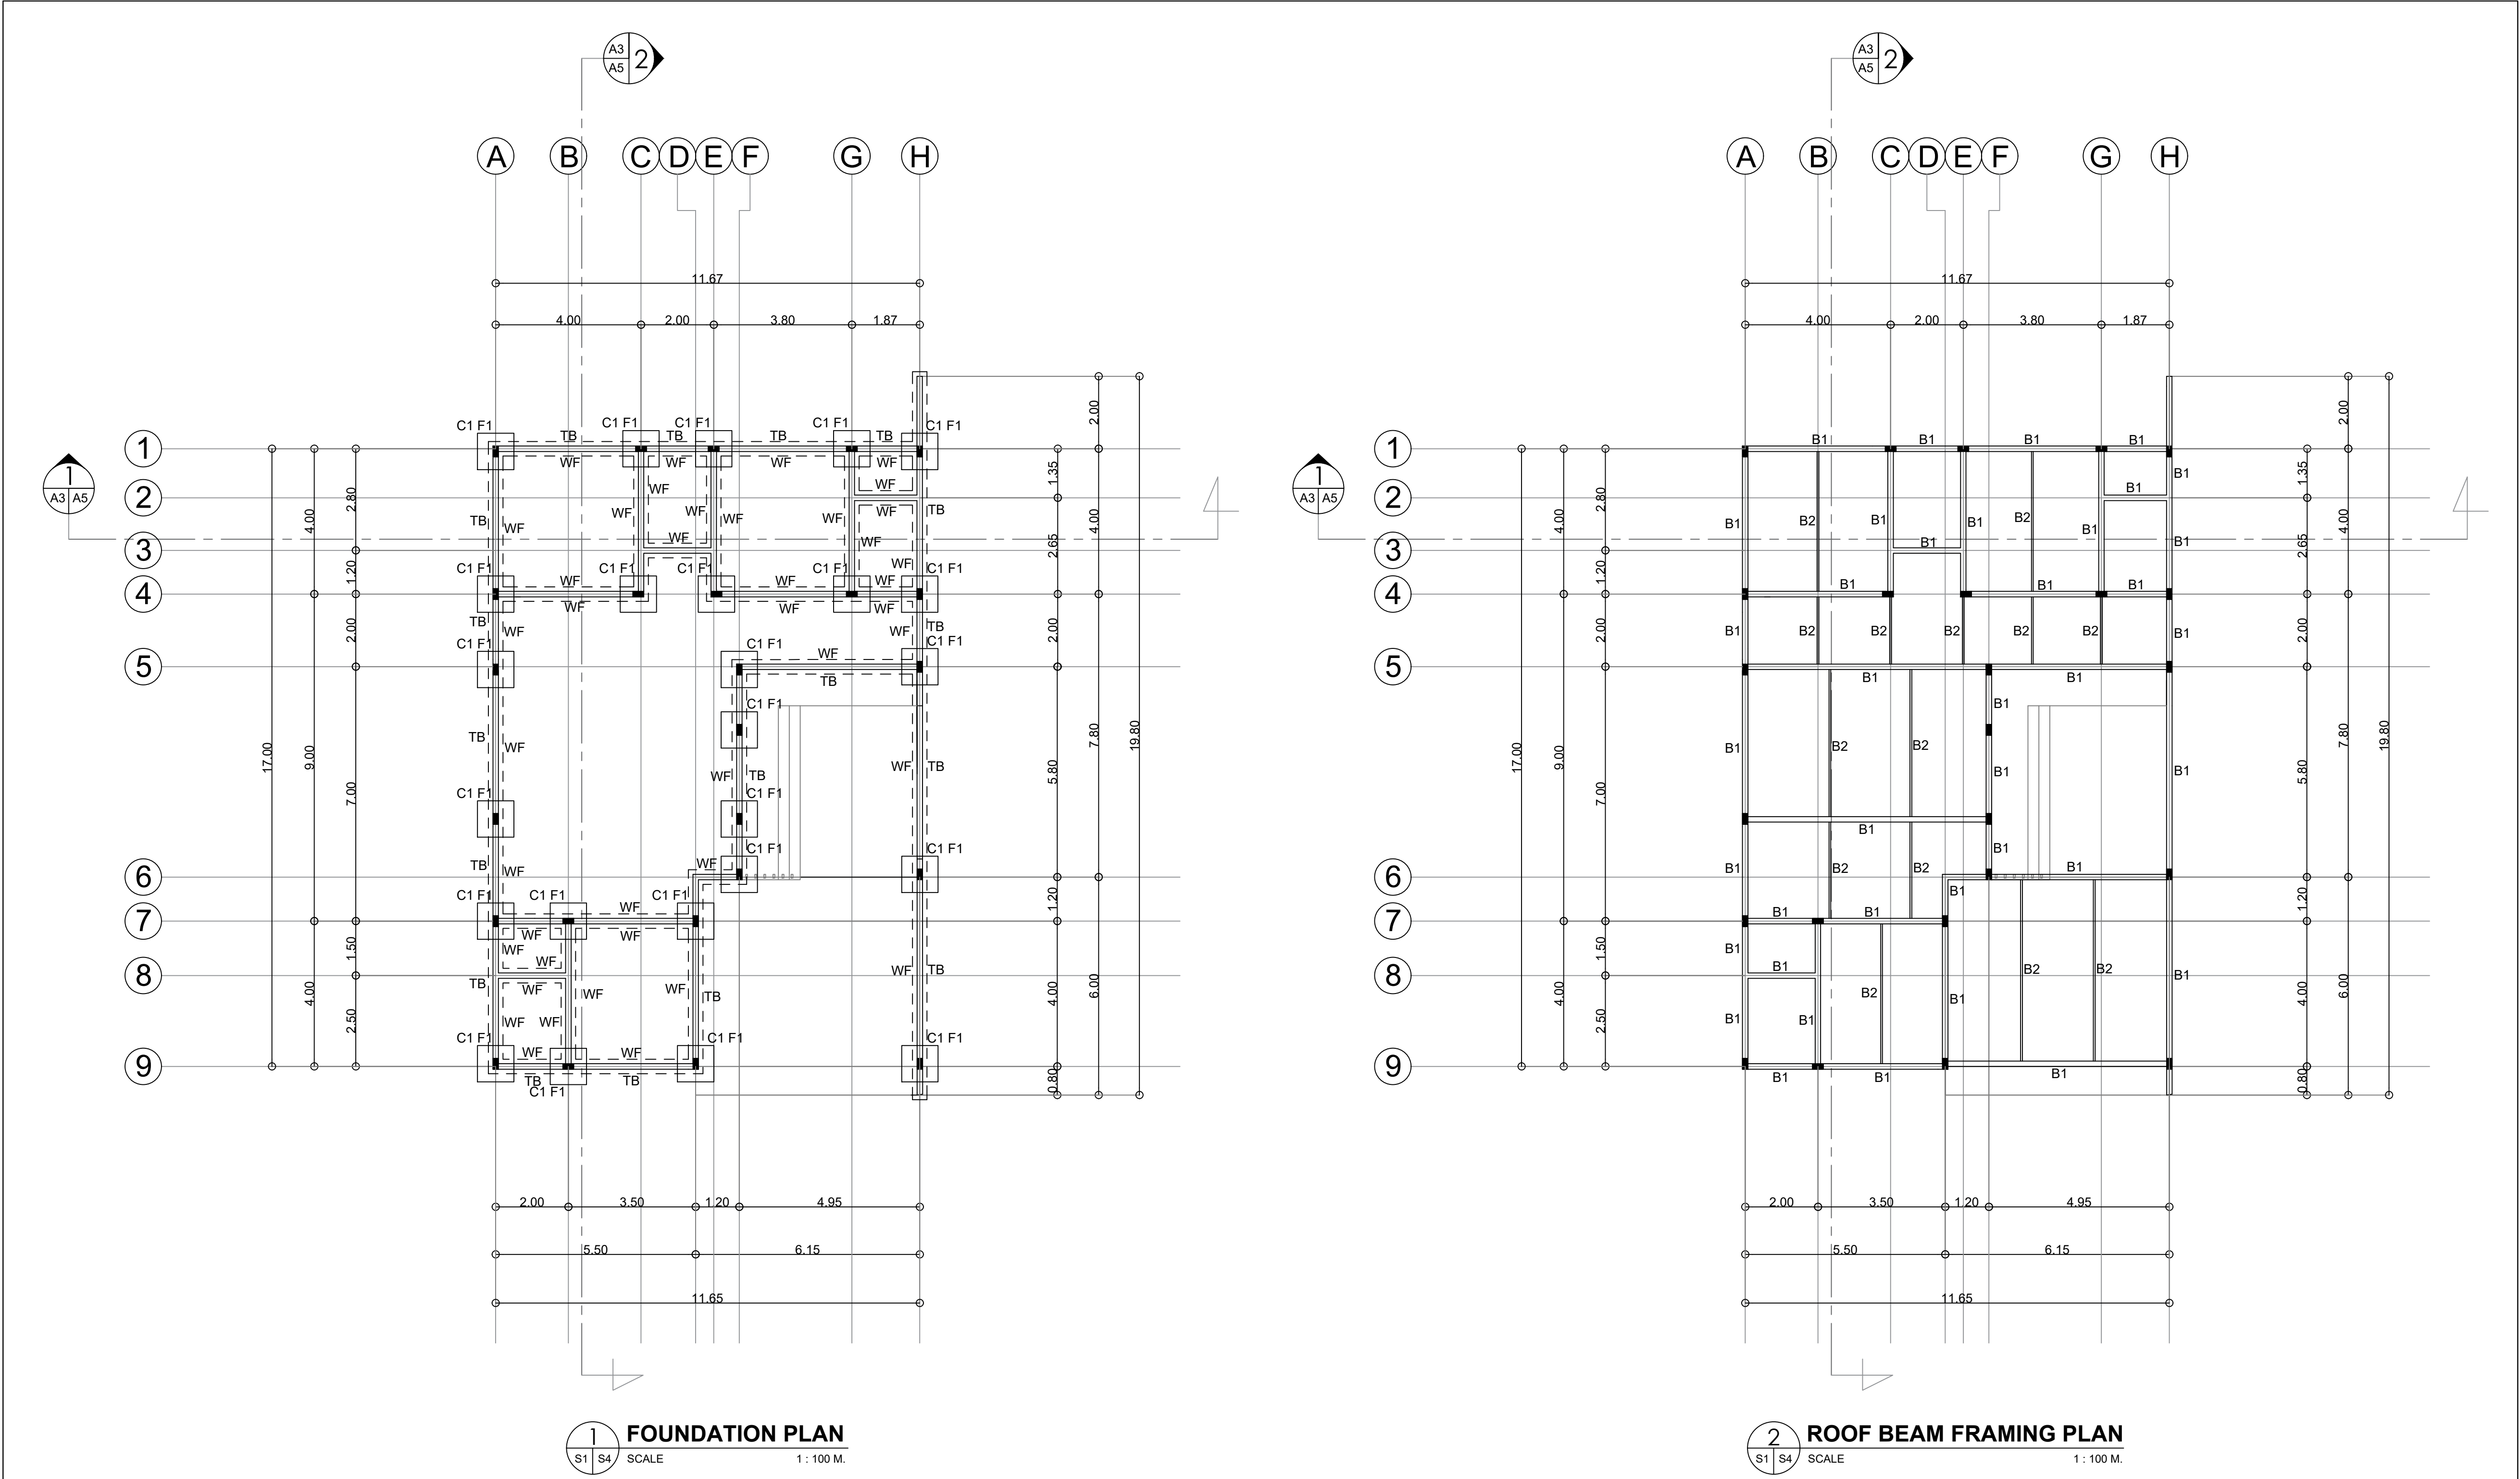

ARCHITECT		ENGINEER	
PRC No.:		PRC No.:	
IAPOA No.:		PTR No.:	
DATE:		DATE:	
PLACE:		TIN:	

RA 9266 (ARCHITECTURE ACT OF 2004)
- SECTION 33






DRAWINGS & SPECIFICATION DULY SIGNED, STAMPED OR SEALED AS INSTRUMENT OF SERVICE ARE THE PROPERTY AND DOCUMENTS OF THE ARCHITECT. WHETHER THE OBJECT FOR WHICH THEY ARE MADE IS EXECUTED OR NOT, IT SHALL BE UNLAWFUL FOR ANY PERSON WITHOUT THE WRITTEN CONSENT OF THE ARCHITECT OR AUTHOR OF THE SAID DOCUMENTS TO DUPLICATE FOR USE IN THE REPETITION & FOR OTHER PROJECTS OR BUILDERS WETHER EXECUTED PARTLY OR IN WHOLE.

PROJECT / LOCATION	OWNER
PROPOSED ONE STOREY RESIDENTIAL BUILDING	

DESIGNED:	No.	REVISIONS	DATE
DRAWN:			
CHECKED:			
DATE:			

SHEET CONTENT
FOUNDATION PLAN ROOF BEAM FRAMING PLAN

SHEET No.	
S-1	
1	4

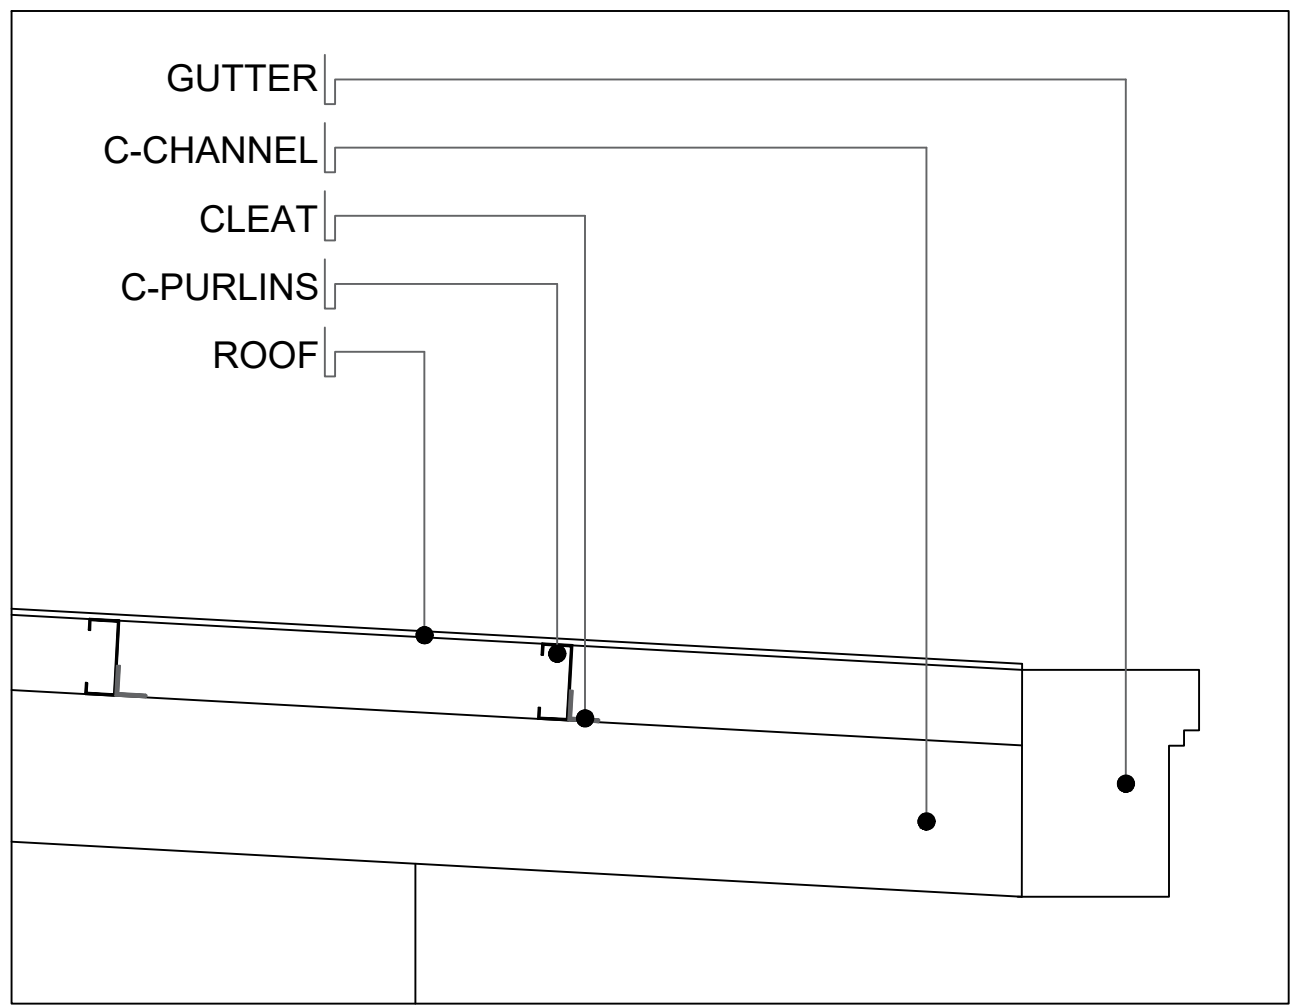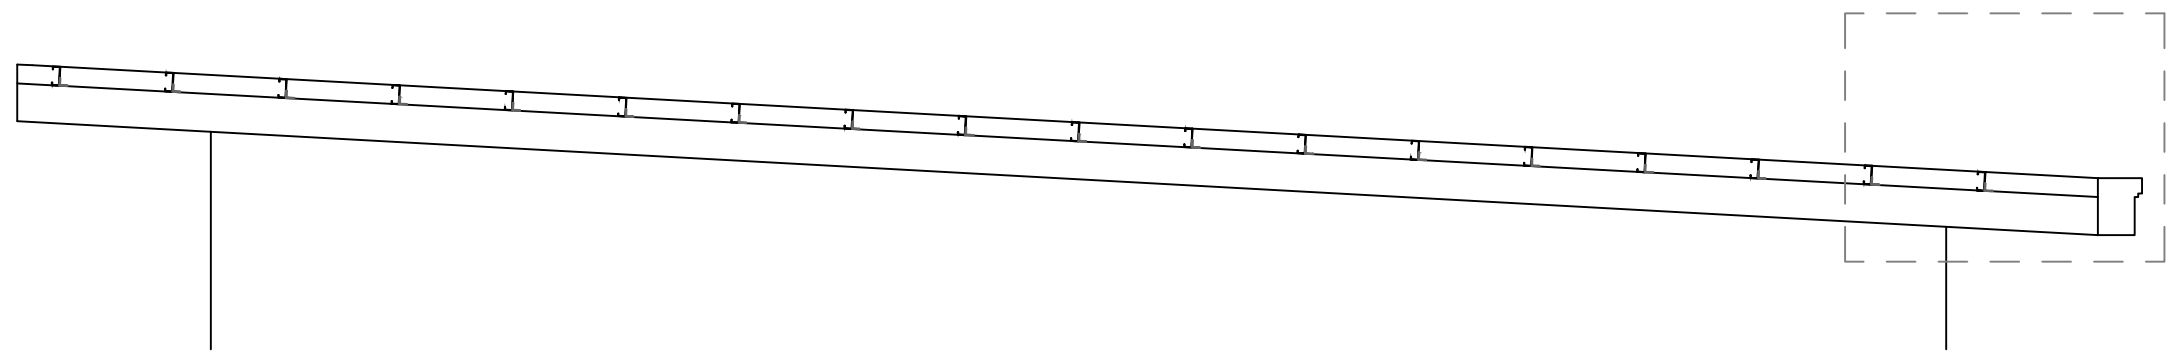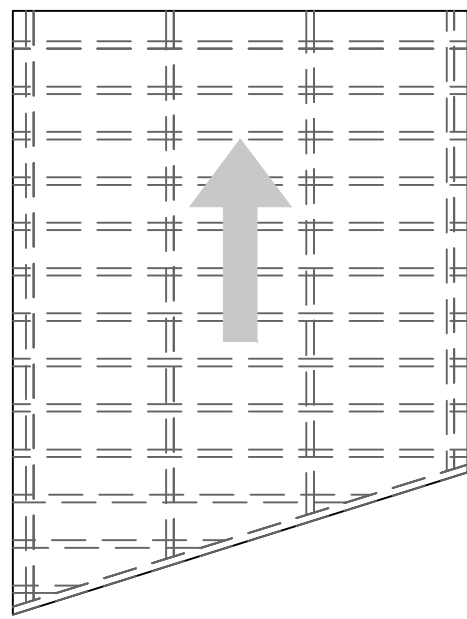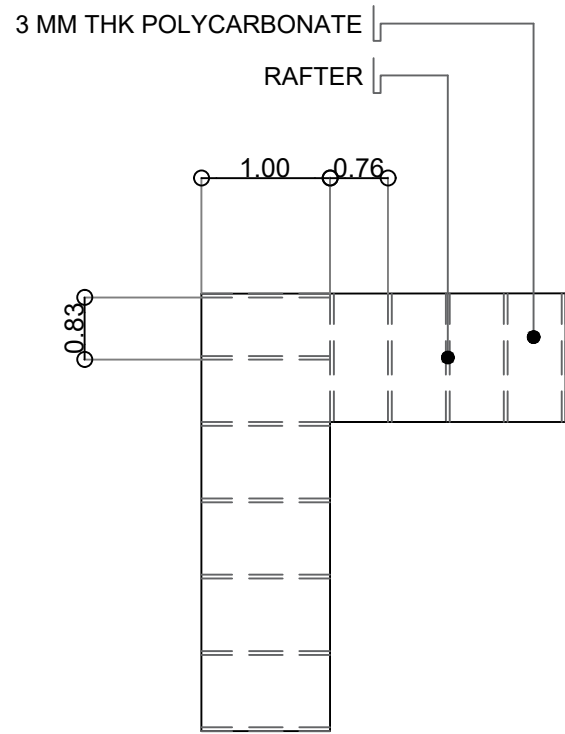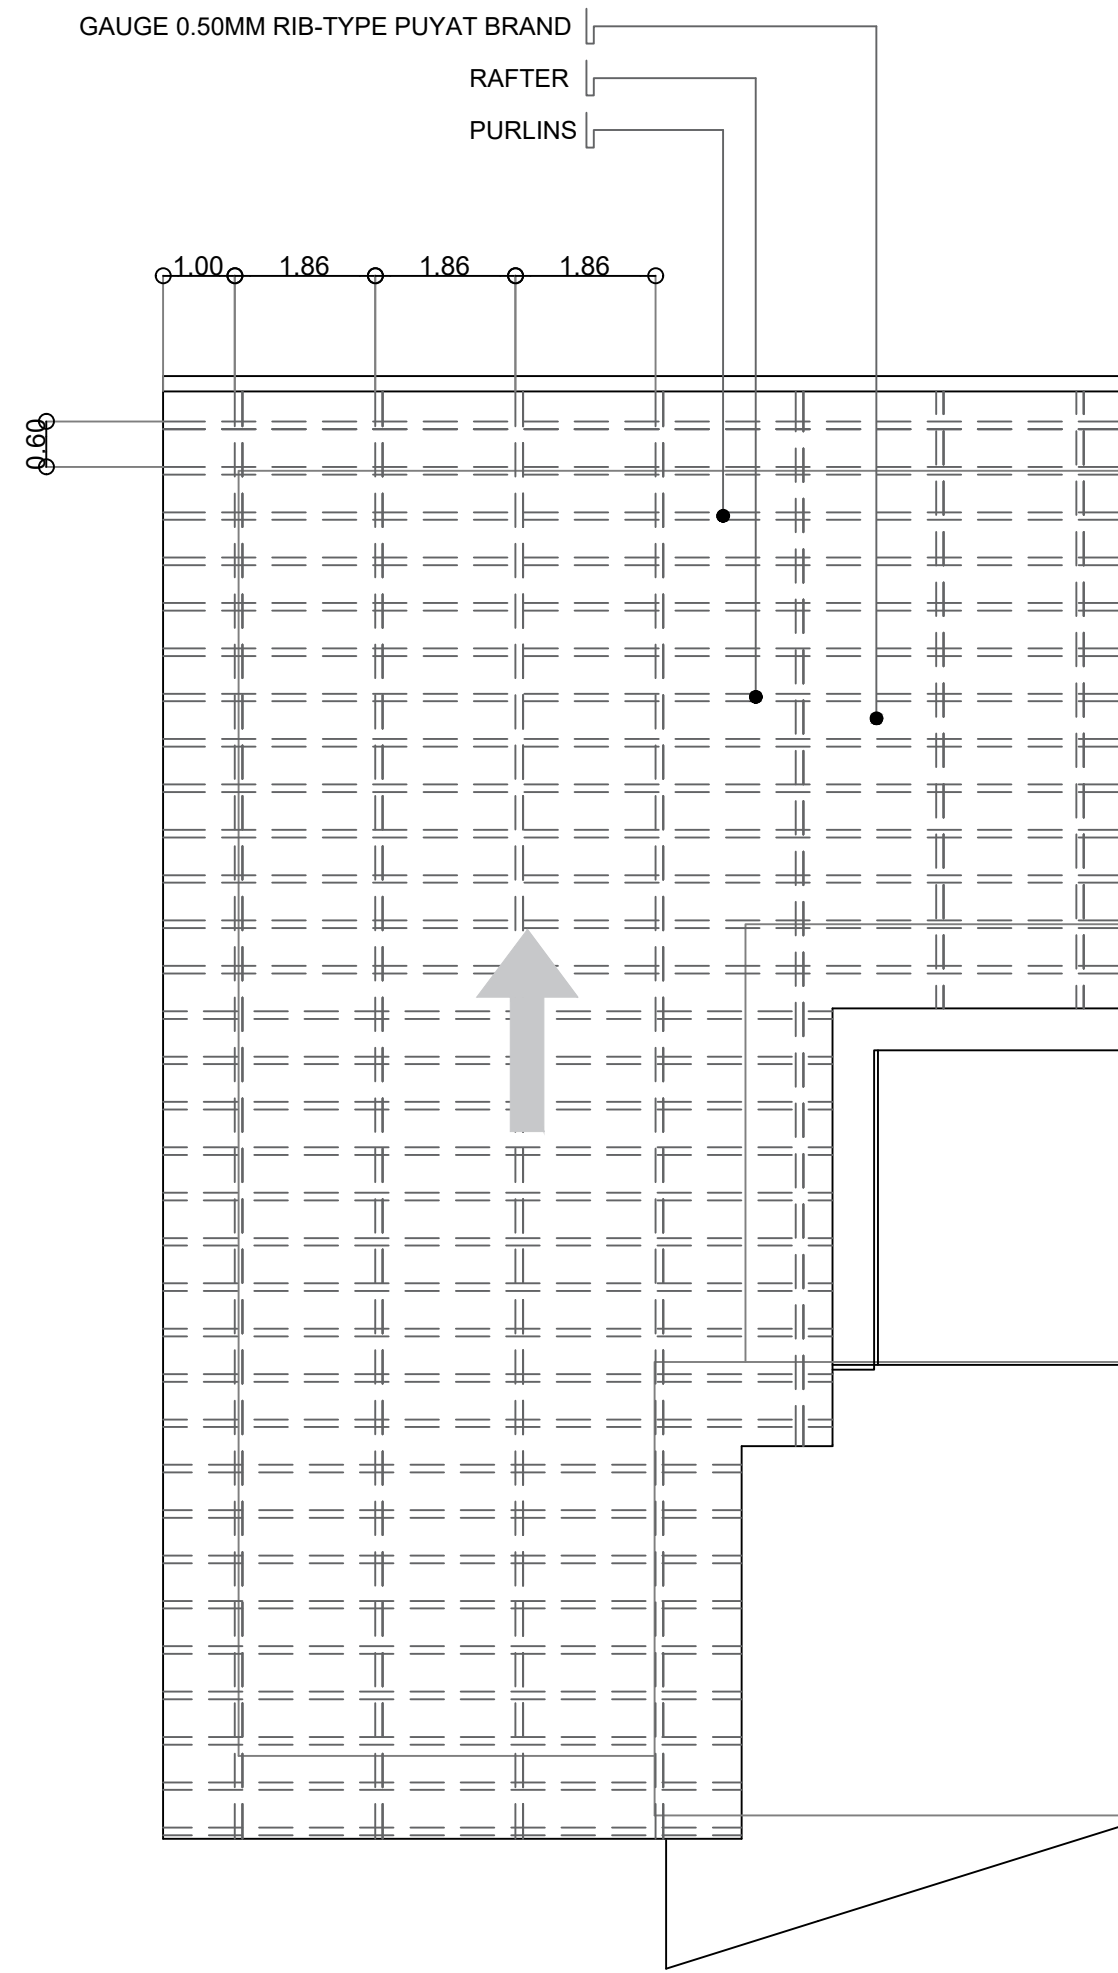

1 ROOF FRAMING PLAN
S2 S4 SCALE 1 : 100 M.

2 ROOF FRAMING DETAILS
S2 S4 SCALE N T S



SALVADOR M. DE GRACIA
CALABANG EAST, SAN LUIS, BATAVIA
09272447115

ARCHITECT		ENGINEER	
PRC No.:		PTR No.:	
IAPOA No.:		DATE:	
PTR No.:		DATE:	
PLACE:		TIN:	

RA 9266 (ARCHITECTURE ACT OF 2004)
- SECTION 33

DRAWINGS & SPECIFICATION DULY SIGNED, STAMPED OR SEALED AS INSTRUMENT OF SERVICE ARE THE PROPERTY AND DOCUMENTS OF THE ARCHITECT. WHETHER THE OBJECT FOR WHICH THEY ARE MADE IS EXECUTED OR NOT, IT SHALL BE UNLAWFUL FOR ANY PERSON WITHOUT THE WRITTEN CONSENT OF THE ARCHITECT OR AUTHOR OF THE SAID DOCUMENTS TO DUPLICATE FOR USE IN THE REPETITION & FOR OTHER PROJECTS OR BUILDERS WETHER EXECUTED PARTLY OR IN WHOLE.

PROJECT / LOCATION
PROPOSED ONE STOREY RESIDENTIAL BUILDING

OWNER

DESIGNED:


DRAWN:

CHECKED:


DATE:

No.	REVISIONS	DATE


SHEET CONTENT		SHEET No.	
ROOF FRAMING PLAN ROOF FRAMING DETAILS		S-2	
		2	4

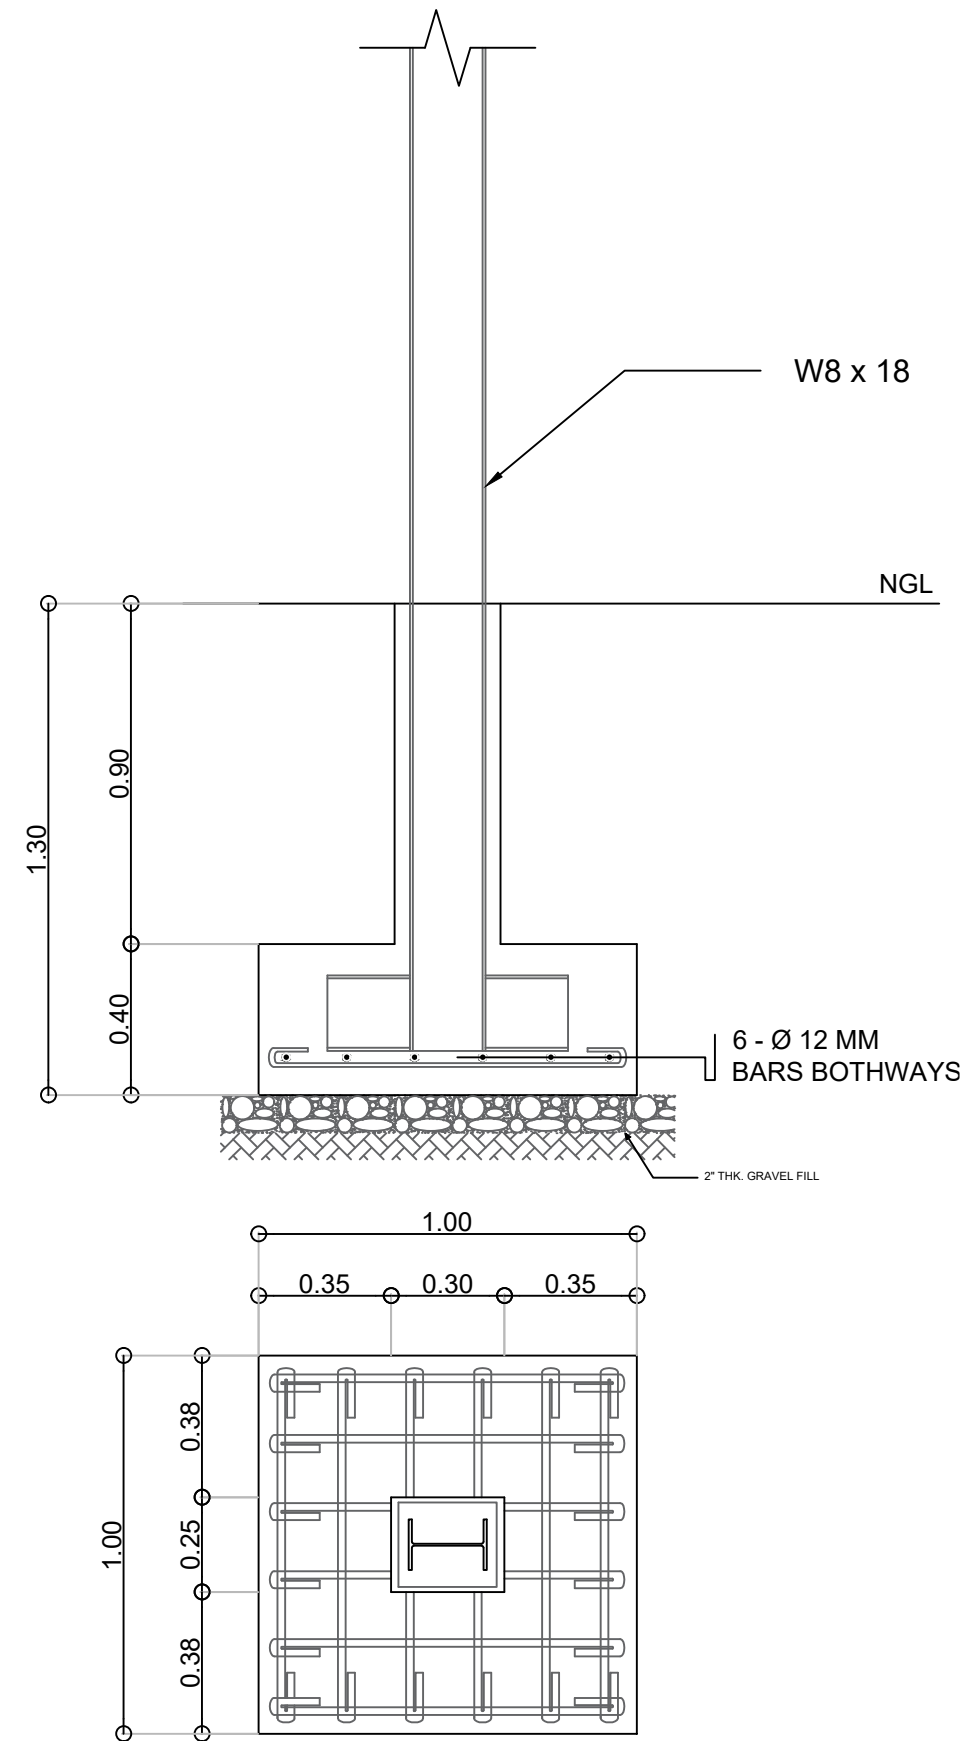


1 COLUMN / FOOTING DETAIL
SCALE 1 : 30 M.

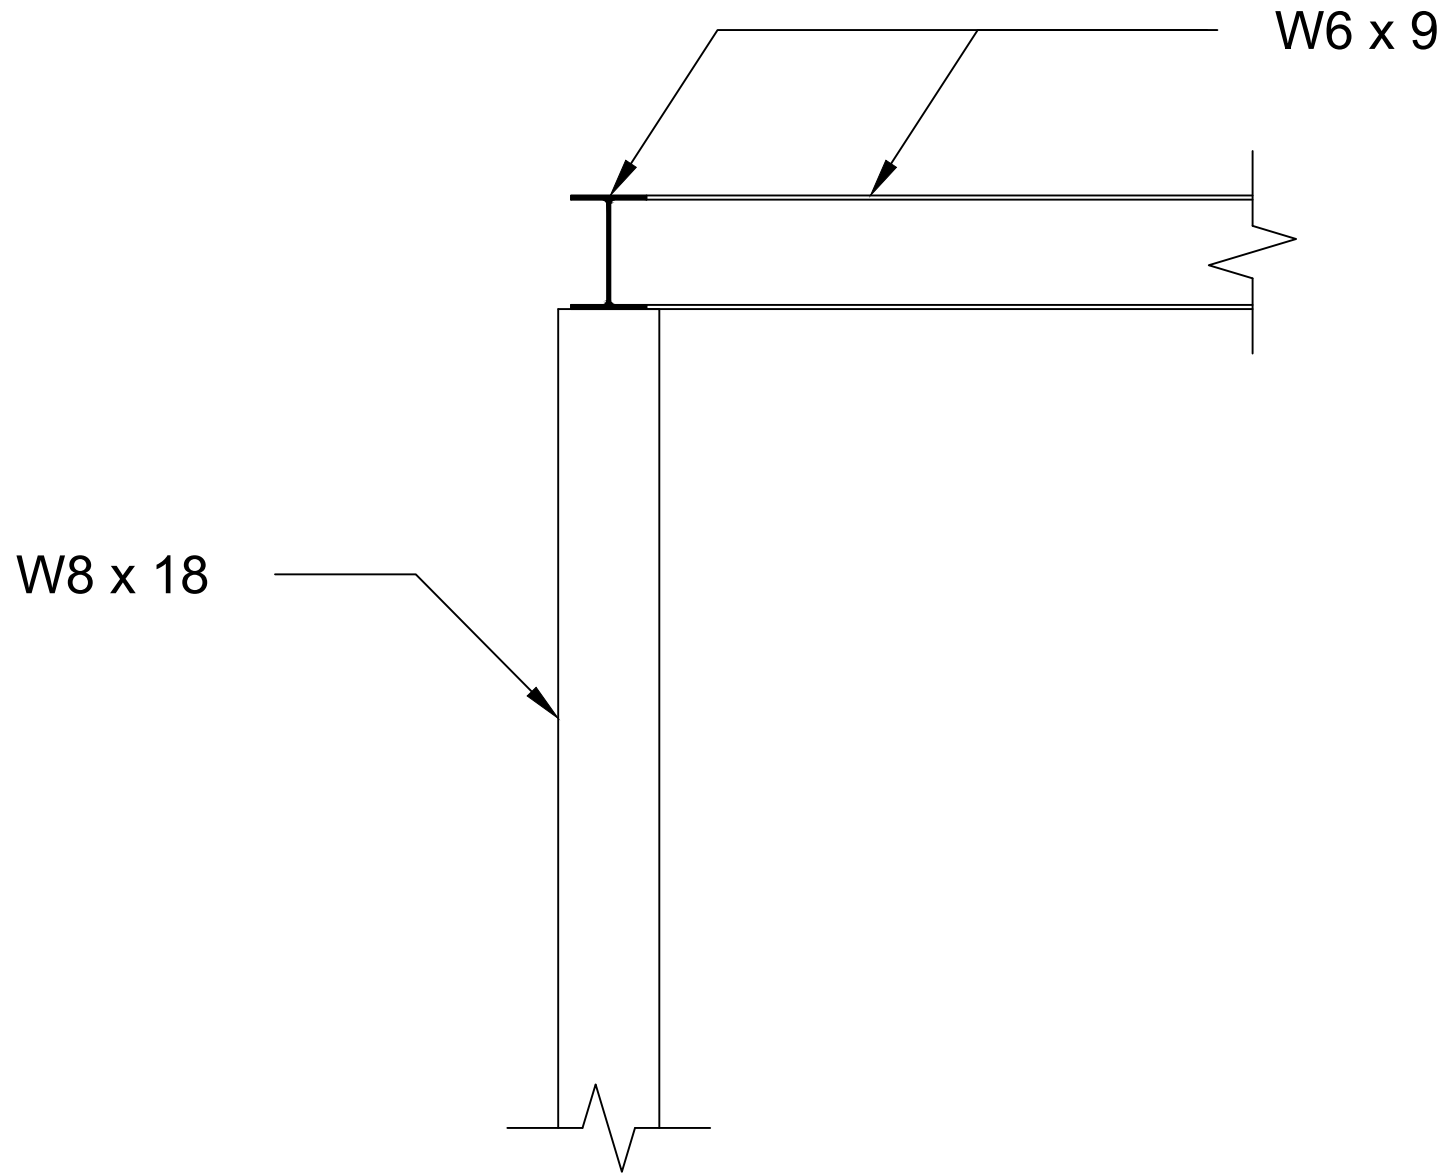


2 COLUMN-BEAM CONNECTION (WELDED)
SCALE 1 : 10 M.

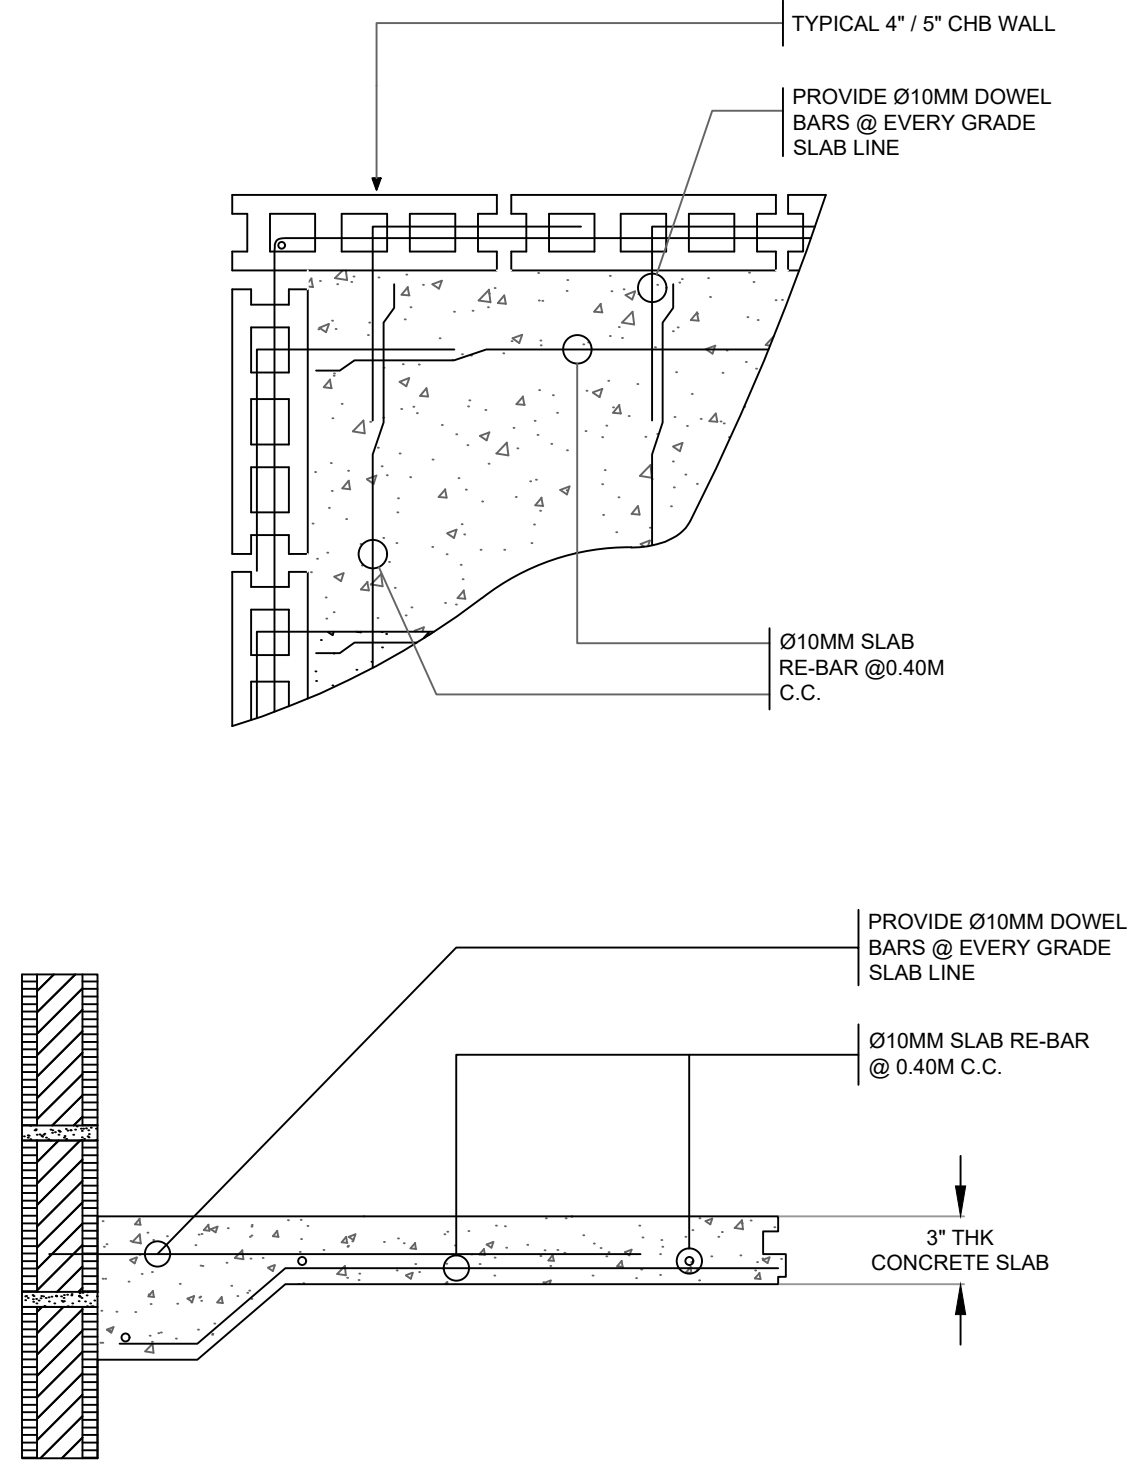


3 SLAB ON GRADE DETAIL
SCALE 1 : 10 M.

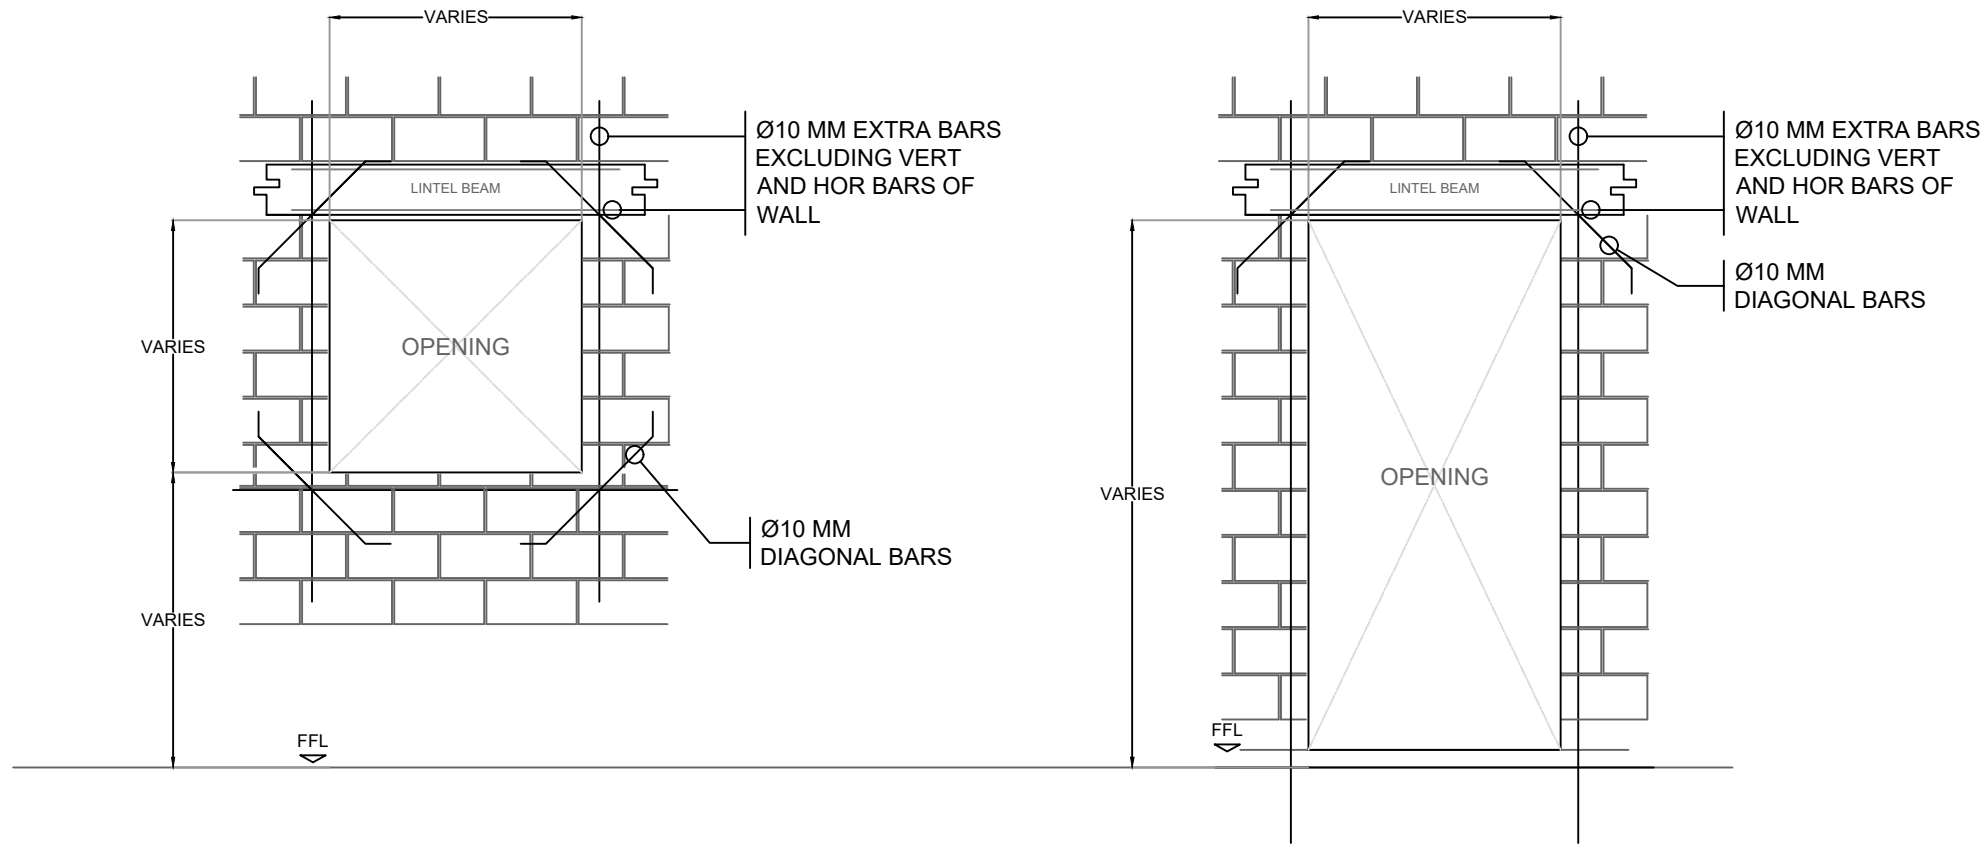

4 DOOR & WINDOW OPENINGS
SCALE 1 : 30 M.

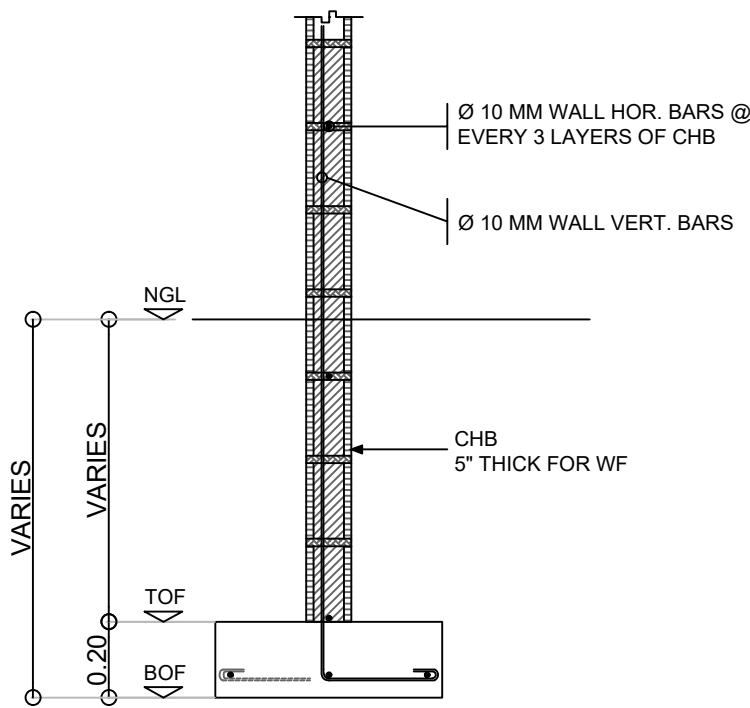

5 WF DETAIL
SCALE 1 : 20 M.

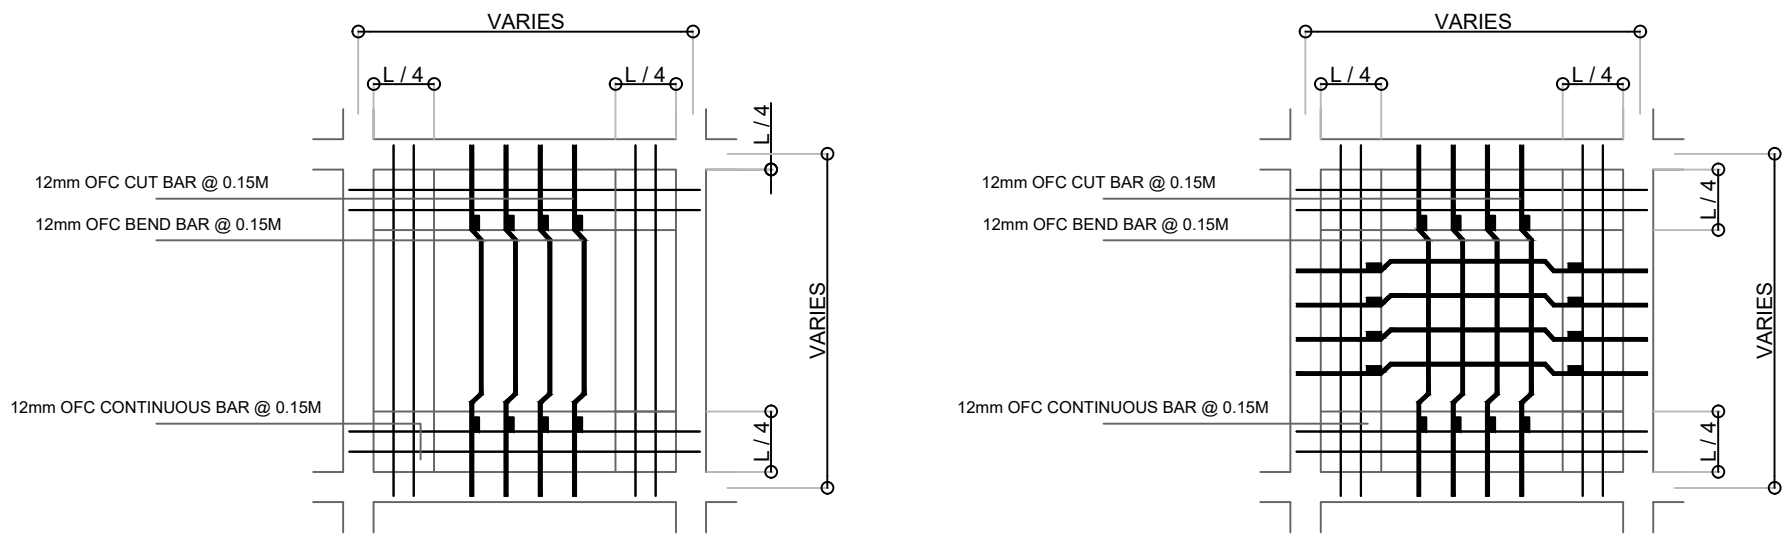

6 SLAB ON GRADE DETAIL
SCALE 1 : 25 M.

 SALVADOR M. DE GRACIA CALUMPANG EAST, SAN LUIS, BATANGAS 09272447151	ARCHITECT		ENGINEER		RA 9266 (ARCHITECTURE ACT OF 2004) - SECTION 33	PROJECT / LOCATION	OWNER	DESIGNED:	No.	REVISIONS	DATE	SHEET CONTENT		SHEET No.	
					DRAWING & SPECIFICATION DULY SIGNED, STAMPED OR SEALED AS INSTRUMENT OF SERVICE ARE THE PROPERTY AND DOCUMENTS OF THE ARCHITECT. WHETHER THE OBJECT FOR WHICH THEY ARE MADE IS EXECUTED OR NOT, IT SHALL BE UNLAWFUL FOR ANY PERSON WITHOUT THE WRITTEN CONSENT OF THE ARCHITECT OR AUTHORITY OF THE SAID DOCUMENTS TO DUPLICATE FOR USE IN THE REPETITION & FOR OTHER PROJECTS OR BUILDERS WETHER EXECUTED PARTLY OR IN WHOLE.	PROPOSED ONE STOREY RESIDENTIAL BUILDING	[REDACTED]	DRAWN:				COLUMN / FOOTING DETAILS SLAB DETAIL SLAB ON GRADE DETAIL OPENING DETAILS		S-3	
	PRC No.:		PTR No.:					CHECKED:							
	IAPOA No.:		DATE:												
	PTR No.:		DATE:												
PLACE:		TIN:		PLACE:	TIN:							3	4		

SCHEDULE OF FOOTING

MARK	DIMENSION (m)		THK	DEPTH	REINFORCEMENT
	X	Y			
F-1	1.00	1.00	0.30	1.00	6 - 12MMØ BOTHWAYS

SCHEDULE OF WALL FOOTING

MARK	DIMENSION (m)		REINFORCEMENT	TIES
	WIDTH	DEPTH		
WF-1	0.40	0.20	3 - 12mm Ø CONTINUOUS BAR	10mmØ @ 0.20 O.C.

SCHEDULE OF TIE BEAM



MARK	DIMENSION (m)		REINFORCEMENT	TIES
	WIDTH	DEPTH		
TB	0.15	0.30	6 - 12mm Ø LONGITUDINAL BARS	10mmØ @ 0.30 O.C.

SCHEDULE OF COLUMN



MARK	DIMENSION (mm)		STEEL SIZE
	WIDTH	DEPTH	
C-1	130	200	W8 x 18

SCHEDULE OF BEAM

MARK	DIMENSION (mm)		STEEL SIZE
	WIDTH	DEPTH	
B-1	100	150	W6 x 9
B-2	100	50	STEEL CHANNEL

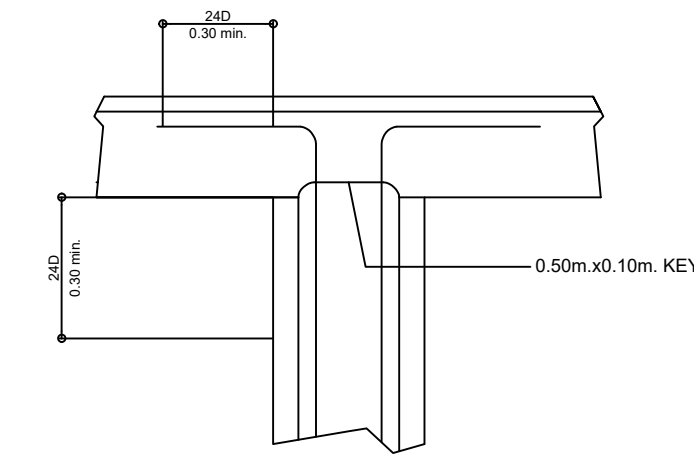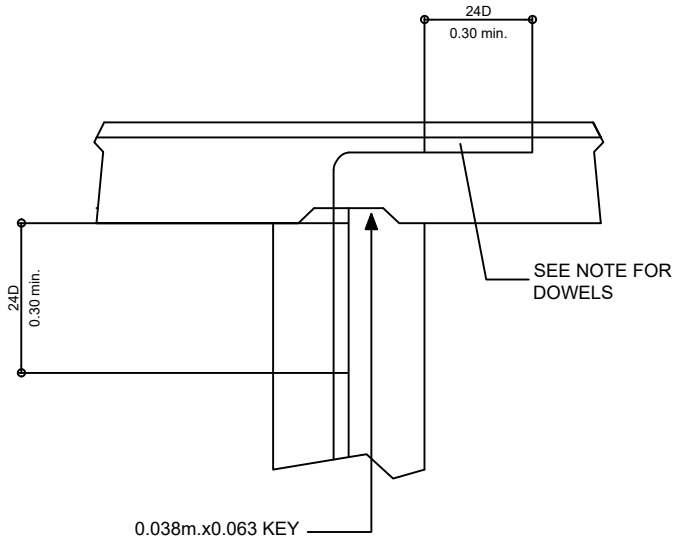


WALL INTERSECTION

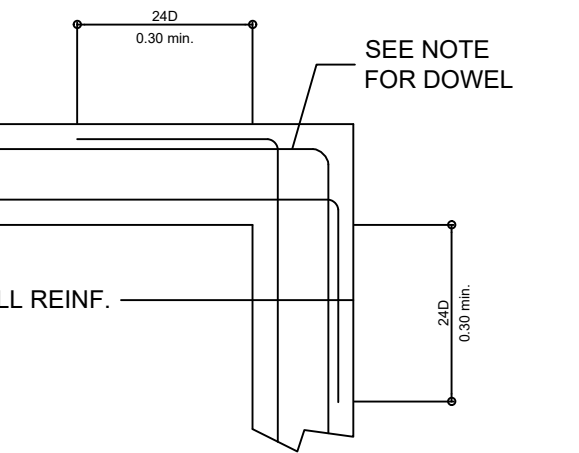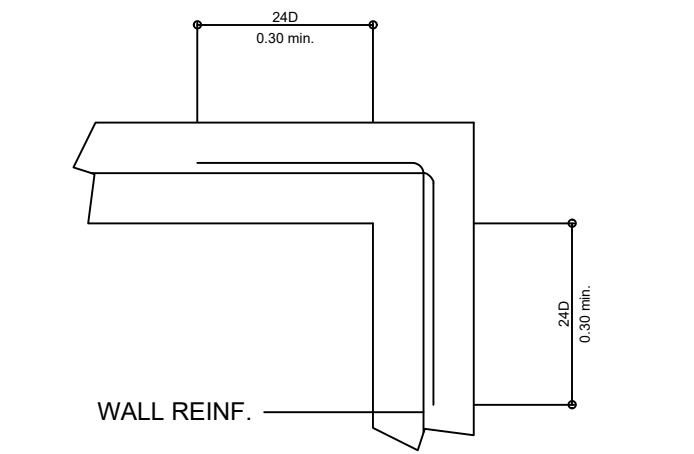

WALL CORNERS

RECOMMENDED SIZES 90° HOOK

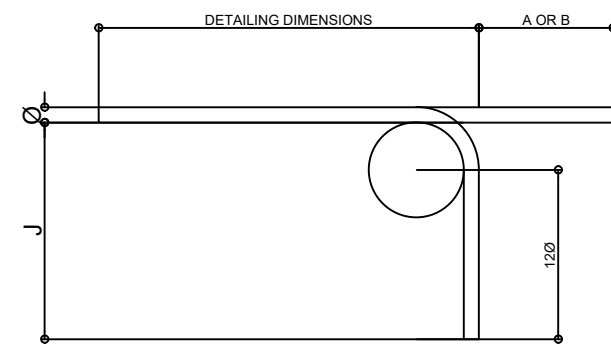

D = 7d FOR M6 TO M20
D = 8d FOR M25 TO M36

BAR SIZE Ø	HOOK A OR B	J
M6	88.9 MM	101.6 MM
M10	139.7 MM	152.4 MM
M12	190.5 MM	215.4 MM
M16	228.6 MM	254.0 MM
M20	266.7 MM	317.5 MM
M25	368.3 MM	431.8 MM
M28	419.1 MM	482.8 MM
M32	469.9 MM	546.1 MM
M36	520.7 MM	609.6 MM

CONSTRUCTION NOTES

GENERAL NOTES

THE CONTRACTOR SHALL VERIFY ALL DIMENSIONS AND CONDITIONS AT THE SITE BEFORE ALL WORK IS TO BEGIN. CHECK WITH OTHER DISCIPLINES AND THE SPECIFICATIONS FOR THE LOCATION AND DIMENSIONS OF DEPRESSIONS, GROOVES, REGLETS, SLEEVES, CIRBS, OPENINGS, PARTITIONS, EMBEDDED OR ATTACHED ITEMS.

THE STRUCTURAL DRAWINGS AND SPECIFICATIONS REPRESENT THE FINISHED STRUCTURES. THEY DO NOT INDICATE THE METHOD OF CONSTRUCTION UNLESS OTHERWISE STATED. THE CONTRACTOR SHALL PROVIDE ALL NECESSARY MEASURES TO PROTECT THE STRUCTURE, ADJACENT PROPERTIES, WORKMEN, AND OTHER PERSONS DURING ALL PHASES OF CONSTRUCTION.

SHOP DRAWINGS WITH ERECTION AND PLACING DIAGRAMMS OF ALL STRUCTURAL ENGINEER'S APPROVAL BEFORE FABRICATION.

THE CONTRACTOR SHALL BE RESPONSIBLE FOR COMPLYING WITH ALL SAFETY PRECAUTIONS AND REGULATIONS DURING THE WORK. THE ENGINEER WILL NOT ADVISE NOR ISSUE DIRECTION AS TO SAFETY PRECAUTIONS AND REGULATIONS.

IT SHALL BE THE CONTRACTOR'S RESPONSIBILITY TO PROVIDE ADEQUATE SHORINGS AND BRACINGS AT THE STRUCTURE FOR ALL LOADS THAT MAYBE IMPOSED DURING CONSTRUCTION.

LOADING CRITERIA

DESIGN GRAVITY DEAD LOADS USED IN THE DESIGN OF THIS STRUCTURE ARE AS FOLLOWS:

- ROOF AND WALL COVERING
METAL ROOFING AND PURLINS 0.200 kPa
METAL TRUSSES 0.770 kPa
- FLOOR FINISHES AND COVERINGS
CERAMIC TILE (20mm) ON 25mm CONCRETE BED 1.100 kPa
- CEILINGS
GYPSUM BOARD, PER mm THICKNESS 0.008 kPa
SUSPENDED STEEL CHANNEL SYSTEM 0.100 kPa
MECHANICAL AND ELECTRICAL FIXTURES 0.150 kPa
- FRAME PARTITIONS & WALLS
PARTITION LOADING (SUBJECT TO CHANGES) 1.000 kPa
- MATERIALS DENSITY
CONCRETE, REINFORCED - STONE (INCL. GRAVEL) 23.600 kN per cu.m.

DESIGN GRAVITY LIVE LOADS USED IN THE DESIGN OF THIS STRUCTURE ARE AS FOLLOWS:

- ROOF LIVE LOAD

ROOF SLOPE	TRIBUTARY AREA (sq.m.)		
	0 - 18.5	18.5 - 56	OVER 56
FLAT - LESS THAN 33%	1.00	0.75	0.60
33% - LESS THAN 100%	0.75	0.70	0.60
100% AND OVER	0.60	0.60	0.60
AWNINGS (EXCEPT CLOTH COVERED)	0.25	0.25	0.25

- FLOOR LIVE LOAD
RESIDENTIAL (BASIC) 1.900 kPa
EXIT FACILITIES 4.800 kPa

DESIGN WIND PRESSURE AND WIND FORCE (SECTION 207 OF NSCP 2001-VOL.1):

where: $q = qz$ $P = q(GCp - qn(GCp))$ AND $F = qz G GFAT$
 qh - FOR WINDWARD WALL AT HEIGHT "Z" ABOVE GROUND
 G - FOR LEEWARD WALL, SIDE WALLS & ROOF AT MEAN ROOF HT;
 Cp - GIVEN IN SECTION 207.6.1 OF NSCP 2001 - VOL. 1
 GCP - GIVEN IN FIGURE 207.3 OF NSCP 2001 - VOL. 1; AND
 Cf - GIVEN IN TABLE 207.4 OF NSCP 2001 - VOL. 1
 At - GIVEN IN TABLES 207-6 TO 207-10
- PROJECTED AREA NORMAL TO WIND

DESIGN SEISMIC FORCE (SECTION 208 OF NSCP 2001 - VOL. 1):
 $V = (Cv I W) / RT$

WHERE: Cv - SEISMIC COEFFICIENT AS SET FORTH IN TABLE 208-1 OF NSCP 2001 - VOL. 1
 I - IMPORTANCE FACTOR GIVEN IN TABLE 208-1 FOR STANDARD OCCUPANCY STRUCTURES OF NSCP 2002 - VOL. 1;
 R - SEISMIC FACTOR AS SET FORTH IN TABLE 208-11 & 208-13 OF NSCP 2001 - VOL. 1
 T - ELASTIC FUNDAMENTAL PERIOD OF VIBRATION AS PER SECTION 205.5.2.2 OF NSCP 2001 - VOL. 1; AND
 W - TOTAL SEISMIC DEAD LOAD;

CONCRETE WORKS AND REINFORCING BARS

CONCRETE & REINFORCING BARS

- ALL CONCRETE SHALL DEVELOP A MINIMUM COMPRESSIVE STRENGTH (f_c) AT THE END OF 28 DAYS WITH CORRESPONDING MAXIMUM SIZE AGGREGATE AND SLUMPS AS FOLLOWS:

LOCATION	f_c	AGGREGATE MAX. SIZE	SLUMP REQUIREMENTS	
			MIN	MAX
FOUNDATION WORKS	20.7 MPa	G-1"	50mm	125mm
LOAD BEARING WALLS;	20.7 MPa	G-3/8"	100mm	175mm
COLUMN, BEAMS; SLABS	20.7 MPa	G-3/4"	25mm	100mm
NON-STRUCTURAL WALLS	17.2 MPa	G-3/8"	100mm	175mm

- ALL REINFORCING BARS SHALL BE DEFORMED WITH A MINIMUM YIELD STRENGTH OF $F_y = 275.0$ MPa (GRADE 40)

CONSTRUCTION JOINTS, CAMBER REQUIREMENTS, LAP SPLICES, INSERTS & CURING

- CONSTRUCTION JOINTS IF UNAVOIDABLE SHALL BE LOCATED AND FORMED SO AS TO LEAST IMPAIR THE STRENGTH AND APPEARANCE OF THE STRUCTURE AND SHALL BE SUBJECT TO THE APPROVAL OF THE ENGINEER.
- SPLICES SHALL BE SECURELY WIRED TOGETHER AND SHALL LAP OR EXTEND WITH APPLICABLE LAP SPLICES AND ANCHORAGE LENGTHS, UNLESS OTHERWISE SHOWN ON DRAWINGS. SPLICES SHALL BE STAGGERED WHENEVER POSSIBLE.

- CAMBER ALL REINFORCED CONCRETE BEAMS AT LEAST 10mm FOR EVERY 4000mm OF CLEAR SPAN EXCEPT CANTILEVERS WHICH SHALL BE 50mm FOR EVERY 3000mm OF CLEAR SPAN. CAMBER ALL REINFORCED CONCRETE SLABS AT LEAST 10mm PER 3000mm OF SHORTER SPAN AND 20mm FOR EVERY 2000mm OF SLABS FOR CANTILEVER SPAN.
- ALL ANCHOR BOLTS, DOWELS AND OTHER INSERTS, SHALL BE PROPERLY POSITIONED AND SECURED IN PLACE PRIOR TO PLACING OF CONCRETE.
- EXPOSED SURFACES OF CONCRETE SHALL BE PROTECTED FROM FOREMATURE DRYING AND KEPT THOROUGHLY MOIST FOR A MINIMUM OF 7 CONSECUTIVE DAYS IMMEDIATELY AFTER POURING.

C. CONCRETE COVER OVER REINFORCING BARS

STRUCTURAL ELEMENT	CLEAR BAR COVER
i. FOOTINGS & OTHER PRINCIPAL STRUCTURAL MEMBERS IN WHICH CONCRETE IS DEPOSITED AGAINST THE GROUND.	75mm
ii. CONCRETE SURFACES EXPOSED TO WEATHER OR GROUND AFTER REMOVAL OF FORMS - FOR BARS MORE THAN 16mm IN DIAMETER - FOR BARS 16mm OR LESS IN DIAMETER	50mm 40mm
iii. CONCRETE SURFACES NOT DIRECTLY EXPOSED TO WEATHER OR GROUND - FOR SLABS, WALLS & JOIST W/ 36mm Ø BARS OR LESS IN DIAMETER - FOR BEAMS, GIRDERS AND COLUMN (PRIMARY REINFORCEMENT, TIES, STIRRUPS, SPIRALS)	20mm 40mm
iv. FOR BUNDLED BARS, THE MIN CONCRETE COVER SHALL BE EQUAL TO THE DIA. OF THE BUNDLED BARS, BUT LESS THAN 50mm.	EQUIVALENT

D. CONDUITS AND PIPES EMBEDDED IN CONCRETE

- ELECTRIC CONDUITS ARE OTHER WHOSE EMBEDMENT IS ALLOWED SHALL NOT WITH THEIR FITTINGS. DISPLACE MORE THAN 4% OF THE AREA OF THE CROSS-SECTION OF A COLUMN ON WHICH STRESS IS CALCULATED OR WHICH IS REQUIRED FOR FIRE PROTECTION.
- VERTICAL PIPES ARE NOT ALLOWED TO PUNCH THROUGH BEAMS OR GIRDERS. SLEEVES, CONDUITS OR OTHER PIPES PASSING THROUGH BEAMS AND GIRDERS SHALL BE OF SUCH SIZE AND IN SUCH LOCATION AS NOT TO IMPAIR SIGNIFICANTLY THE STRENGTH OF THE CONSTRUCTION.
- EMBEDDED CONDUITS IN SOLID SLABS, UNLESS OTHERWISE NOTED, SHALL BE RUN GENERALLY AT MID BAY AND PARALLEL CONDUITS SHALL BE AT 3-DIAMETERS ON CENTER. CONDUIT SHALL NOT EXCEED $\frac{1}{2}$ OF THE SLAB THICKNESS AND SHALL BE LOCATED AT MID THICKNESS AND SHALL BE LOCATED AT MID THICKNESS OF THE SLAB.
- FORM WORKS AND SHORING
- FORM WORKS SHALL CONFORM TO THE SHAPE, DIMENSION AND SET TRUE TO LINE AND GRADE AND SO CONSTRUCTED AND FASTENED AS TO PRODUCE THE REQUIRED LINES, PLANES AND ELEVATIONS.
- ALL FORMS SHALL BE TREATED WITH APPROVED OIL OR SATURATED WITH WATER IMMEDIATELY BEFORE DEPOSITING OF CONCRETE.
- CONCRETE FOOTINGS MAY BE PLACED IN EXCAVATIONS WITHOUT FORMS UPON INSPECTION AND APPROVAL BY THE ENGINEER.
- DO NOT PERMIT ELEMENTS TO DEFLECT OR ACCEPT LOADS DURING FORM STRIPPING OR RESHORING. PERFORM RESHORING OPERATION TO PREVENT SUBJECTING CONCRETE MEMBERS TO OVERLOADS, ECCENTRIC LOADING, OR REVERSE BENDING. RESHORING ELEMENTS SHALL HAVE THE SAME LOAD-CARRYING CAPABILITIES AS ORIGINAL SHORING AND SHALL BVE SPACED SIMILAR TO ORIGINAL SHORING. FIRMLY SECURE AND BRACE RESHORING ELEMENTS TO PROVIDE SOLID BEARING AND SUPPORT.

FOUNDATION, EXCAVATION AND FILL

- ALL FOOTINGS WERE DESIGNED FOR AN ASSUMED BEARING CAPACITY OF SOIL OF 100 kPa. THE CONTRACTOR SHALL INVESTIGATE AND REPOST TO THE ENGINEER THE ACTUAL SOIL CONDITION AT THE ELEVATION OF THE BOTTOM OF FOOTING TO DETERMINE WHETHER DESIGN BEARING CAPACITY OF THE SOIL CAN BE DEVELOPED OR NOT IN WRITING BEFORE DEPOSITING CONCRETE. ACTUAL SUB-SOIL INVESTIGATION AND TEST SHALL BE UNDERTAKEN IF NECESSARY.
- FOUNDATION SHALL REST ON NATURAL SOIL, DENSE SAND OR VERY HARD CLAY, UNLESS OTHERWISE NOTED BY THE ENGINEER. NO PART OF THE FOUNDATION SHALL REST ON FILL.
- WHERE LOOSE OR SOFT MATERIAL IS ENCOUNTERED AT DEPTH OF FOOTING EMBEDMENT INDICATED, EXCAVATION SHALL CONTINUE UNTIL SUCH FIRM LAYER WITH SAFE BEARING CAPACITY IS OBTAINED. SUCH OVER EXCAVATION SHALL BE REPLACED WITH WELL COMPACTED CRUSHED ROCK OR SELECTED BACKFILL TO 95% OF MAXIMUM DRY DENSITY BASED ON ASTM D-698.
- FILL AND SUBGRADES UNDER FOOTINGS AND SLABS SHALL BE PLACED IN150mm LAYERS AND EACH LAYER SHALL BE COMPACTED TO 95% MAXIMUM DRY DENSITY BEFORE SUBSEQUENT LAYERS ARE TO BE LAID.

STRUCTURAL STEEL

A. MATERIALS, FABRICATION, ERECTION AND QUALITY CONTROL

- STEEL TO BE USED FOR FABRICATION AND ERECTION OF THIS STRUCTURE SHALL COMPLY WITH ALL THE PERTINENT PROVISIONS OF NSCP & AISC SPECIFICATION FOR THE DESIGN, FABRICATION AND ERECTION OF STRUCTURAL STEEL FOR BUILDINGS.
- ALL STRUCTURAL STEEL SHALL HAVE A MAXIMUM YIELD STRENGTH OF 248MPa. WIDE FLANGE, ANGLES, CHANNELS, PLATES SHALL BE ASTM A36. BUILT UP MEMBERS SHALL BE ASTM A36
- ALL BOLTS, NUTS, AND WASHERS SHALL CONFORM TO A307 OR A 325 UNLESS OTHERWISE INDICATED. ANCHOR BOLTS SHALL LIKEWISE BE OF EQUAL STRENGTH AS A325 BOLTS OF THE SAME SIZE.
- ALL WELDS SHALL BE IN ACCORDANCE WITH AWS STRUCTURAL WELD CODE D1-1 LATEST REVISION FOR SHIELDED METAL ARC WELDING PROCESS. ELECTRODES E-70 SHALL CONFORM TO AWS AS-1 OR LATEST EDITION. SUBMERGED ARC WELDING PROCESS MAY BE USED AT THE OPTION OF FABRICATOR UPON THE APPROVAL OF ENGINEER. ALL WELDED CONNECTIONS SHALL DEVELOP THE FULL STRENGTH OF THE MEMBERS CONNECTED.
- BRACING - THE FRAME OF STEEL STRUCTURE SKELETON SHALL BE CARRIED UP TO AND PLUMB WITHIN THE LIMITS DEFINED IN THE AISC CODE OF STANDARD PRACTICE. TEMPORARY BRACING SHALL BE PROVIDED TO RESIST ALL LOADS INCLUDING ERECTION EQUIPMENT.
- ALIGNMENT - NO RIVETTING, PERMANENT BOLTING OR WELDING SHALL BE DONE UNTIL STRUCTURE HAS BEEN PROPERLY ALIGNED.
- STEEL TO BE USED FOR ERECTION OF THIS STRUCTURE SHALL BE PAINTED AND ITS SURFACE PREPARED IN COMPLIANCE WITH THE SPECIFICATIONS.




ARCHITECT		ENGINEER	
PRC No.:		RA 9266 (ARCHITECTURE ACT OF 2004) - SECTION 33	
IAPOA No.:		DRAWINGS & SPECIFICATION DULY SIGNED, STAMPED OR SEALED AS INSTRUMENT OF SERVICE ARE THE PROPERTY AND DOCUMENTS OF THE ARCHITECT. WHETHER THE OBJECT FOR WHICH THEY ARE MADE IS EXECUTED OR NOT, IT SHALL BE UNLAWFUL FOR ANY PERSON WITHOUT THE WRITTEN CONSENT OF THE ARCHITECT OR AUTHOR OF THE SAID DOCUMENTS TO DUPLICATE FOR USE IN THE REPETITION & FOR OTHER PROJECTS OR BUILDERS WETHER EXECUTED PARTLY OR IN WHOLE.	
PTR No.:	DATE:	PTR No.:	DATE:
PLACE:	TIN:	PLACE:	TIN:

PROJECT / LOCATION	
PROPOSED ONE STOREY RESIDENTIAL BUILDING	


OWNER	

DESIGNED:	No.	REVISIONS	DATE
DRAWN:			
CHECKED:			
DATE:			

SHEET CONTENT		SHEET No.	
SCHEDULE OF COLUMN SCHEDULE OF BEAMS DETAILS NOTES & SPECIFICATIONS		S-4	
		4	4

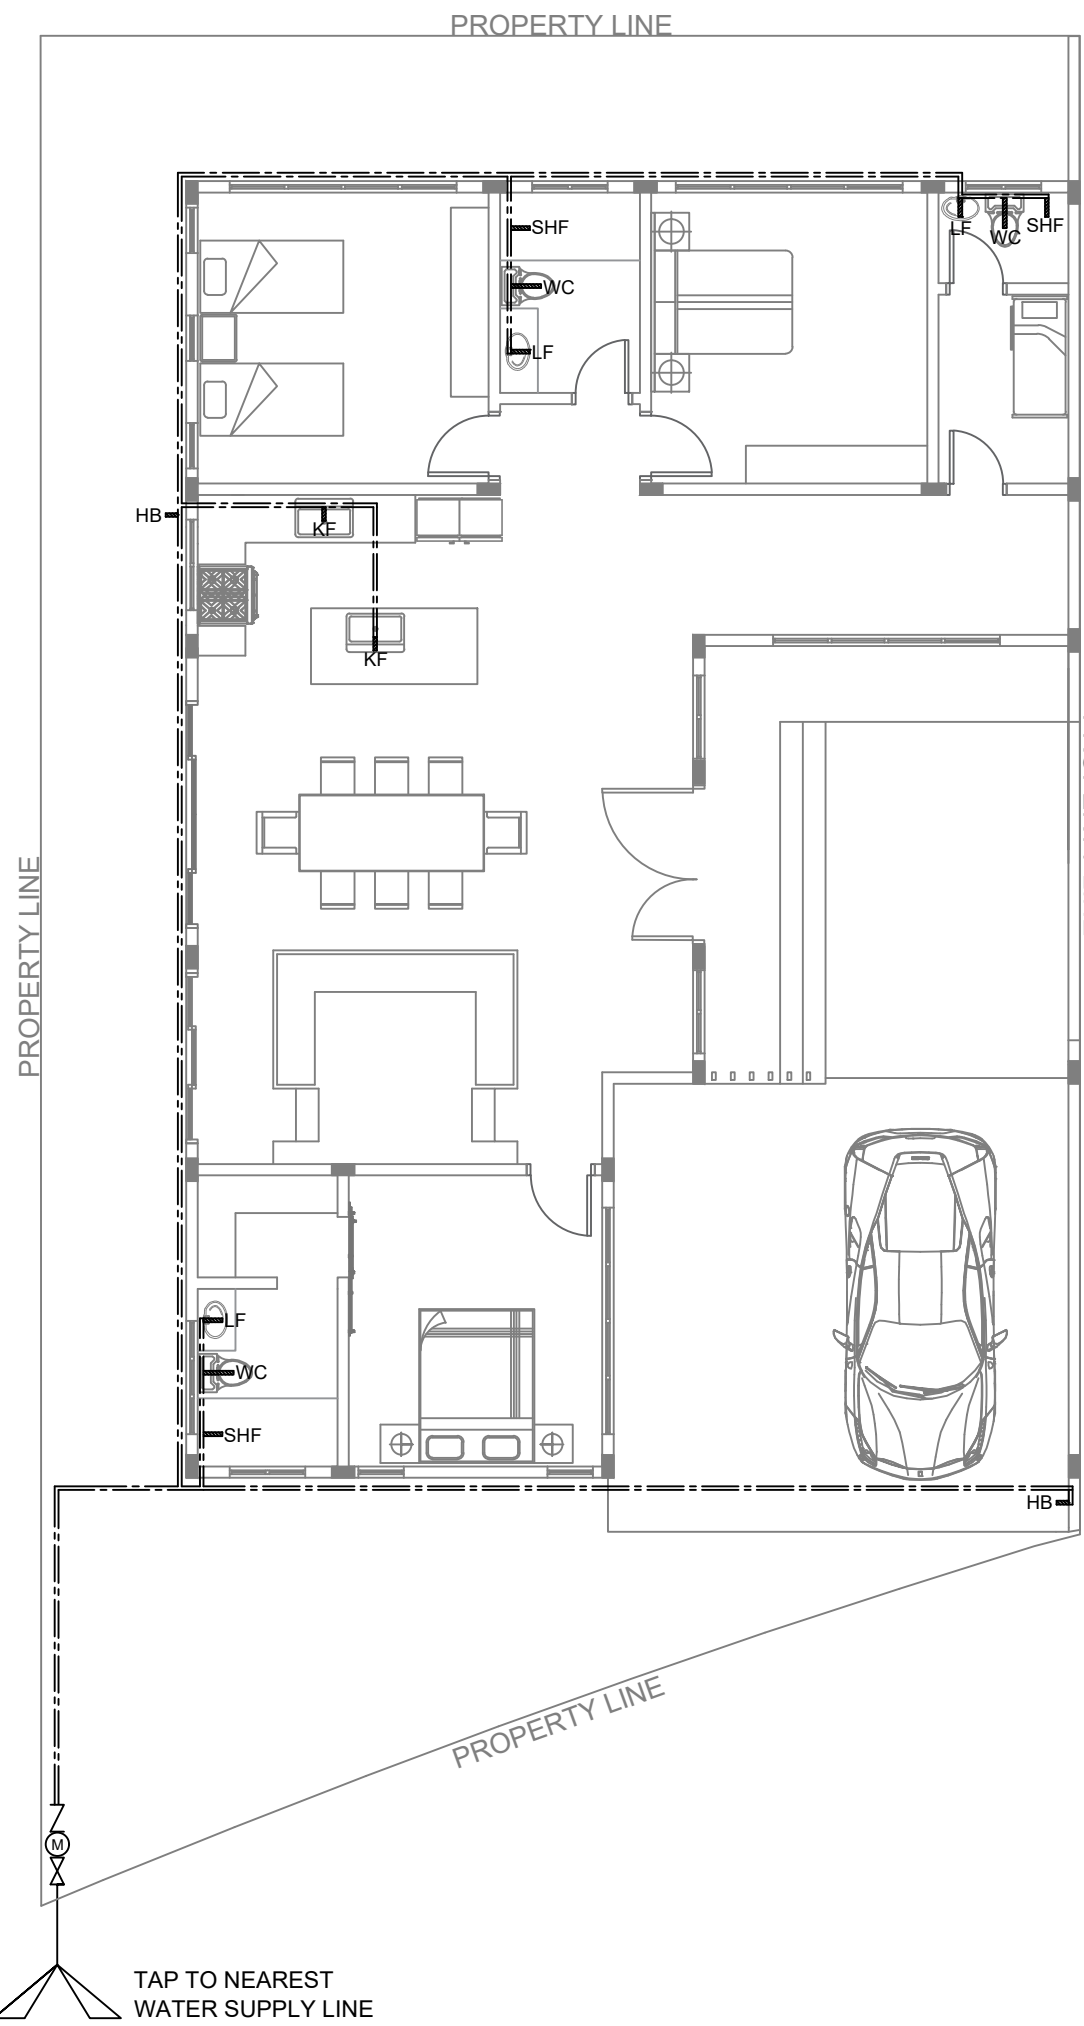


1 WATER DISTRIBUTION LAYOUT
P1 P1 SCALE 1 : 100 M.

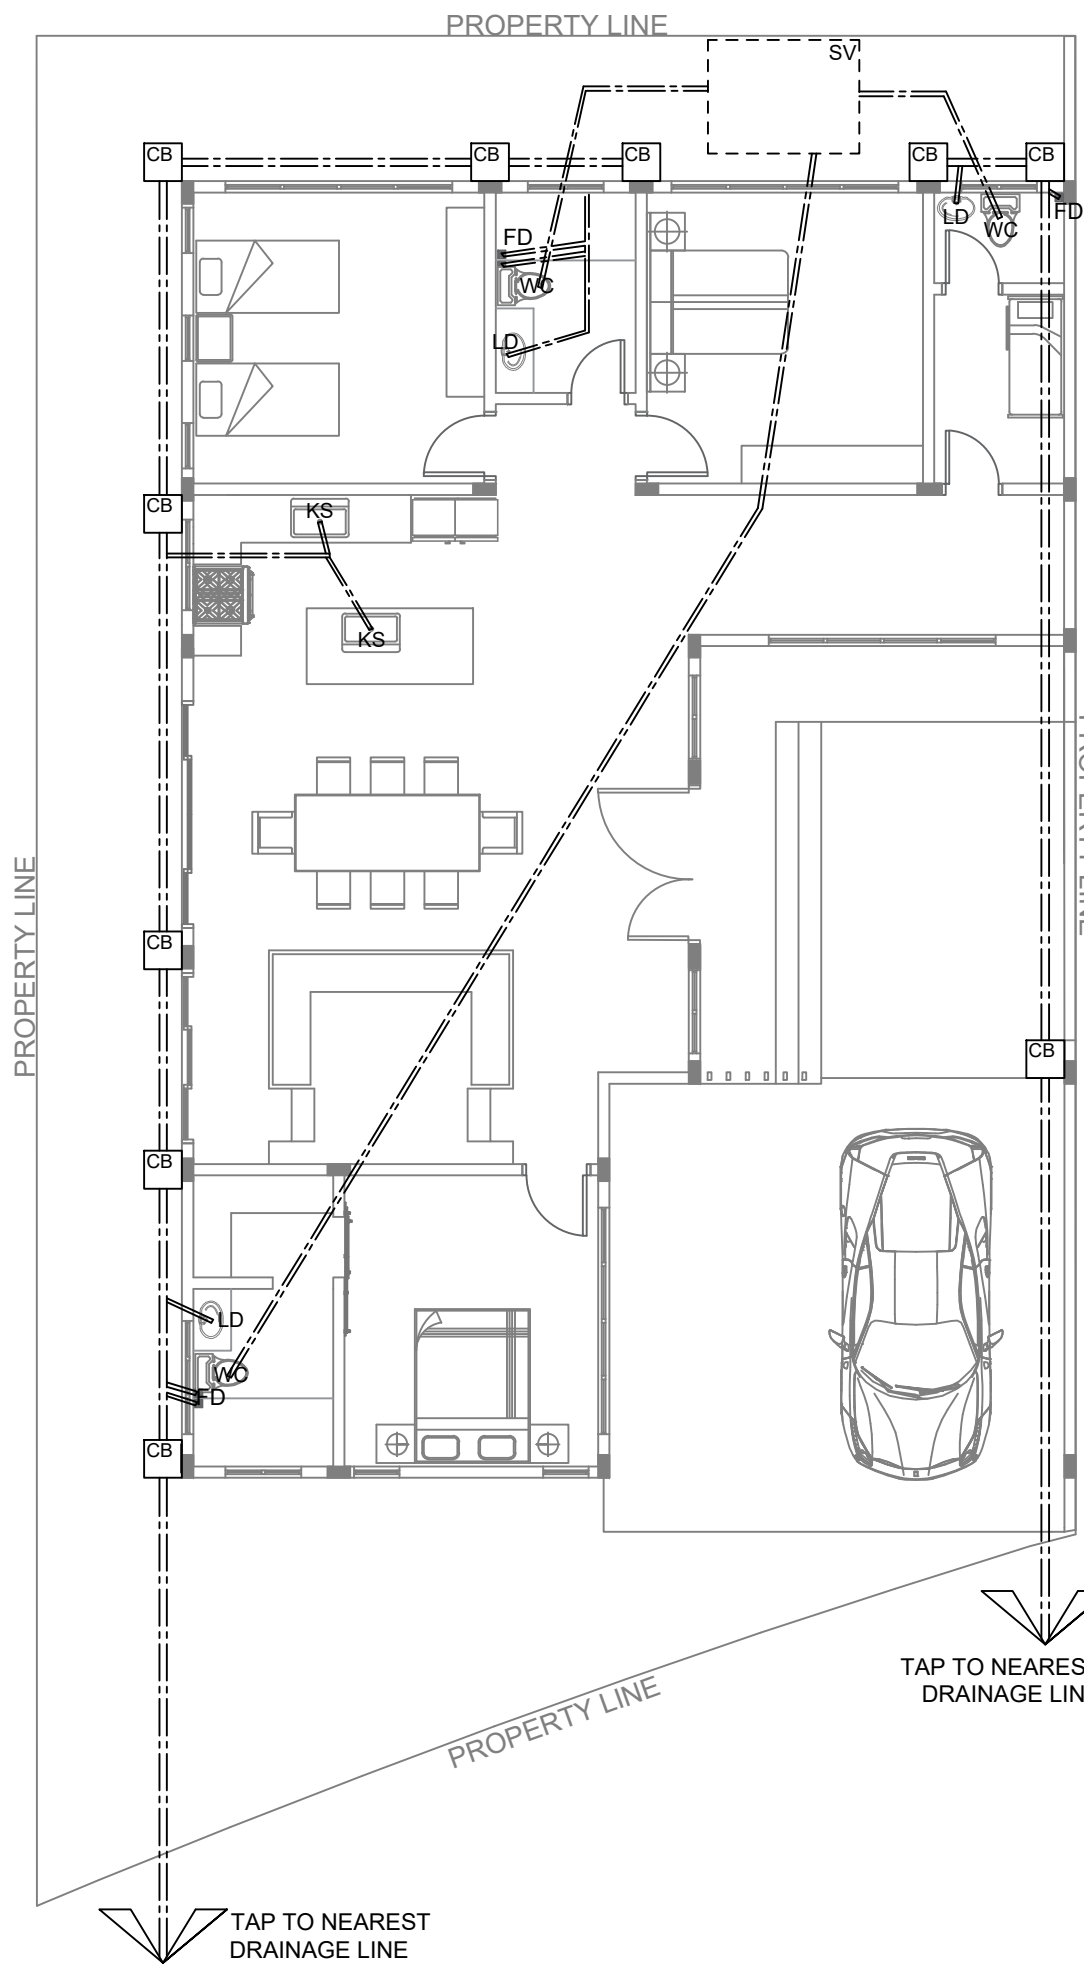


2 SANITARY LAYOUT
P1 P1 SCALE 1 : 100 M.

LEGEND:

ABBR	DESCRIPTION
LF	LAVATORY FAUCET
HB	HOSE BIBB
SHF	SHOWER HEAD FAUCET
KF	KITCHEN FAUCET
WC	WATER CLOSET
LD	LAVATORY DRAIN
KS	KITCHEN SINK
VTR	VENT THRU ROOF
SV	SEPTIC VAULT
MH	MANHOLE
CO	CLEAN OUT
FD	FLOOR DRAIN
WH	WATER HEATER
GV	GATE VALVE
CV	CHECK VALVE
FD	FLOOR DRAIN
M	WATER METER
BF	BATHTUB FAUCET
BD	BATHTUB DRAIN
RD	ROOF SLAB DRAIN

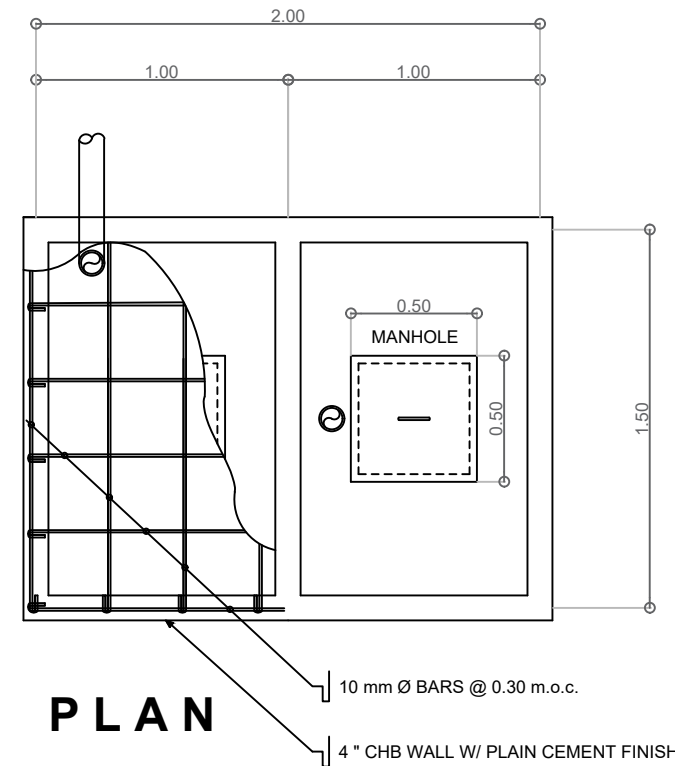


PLAN

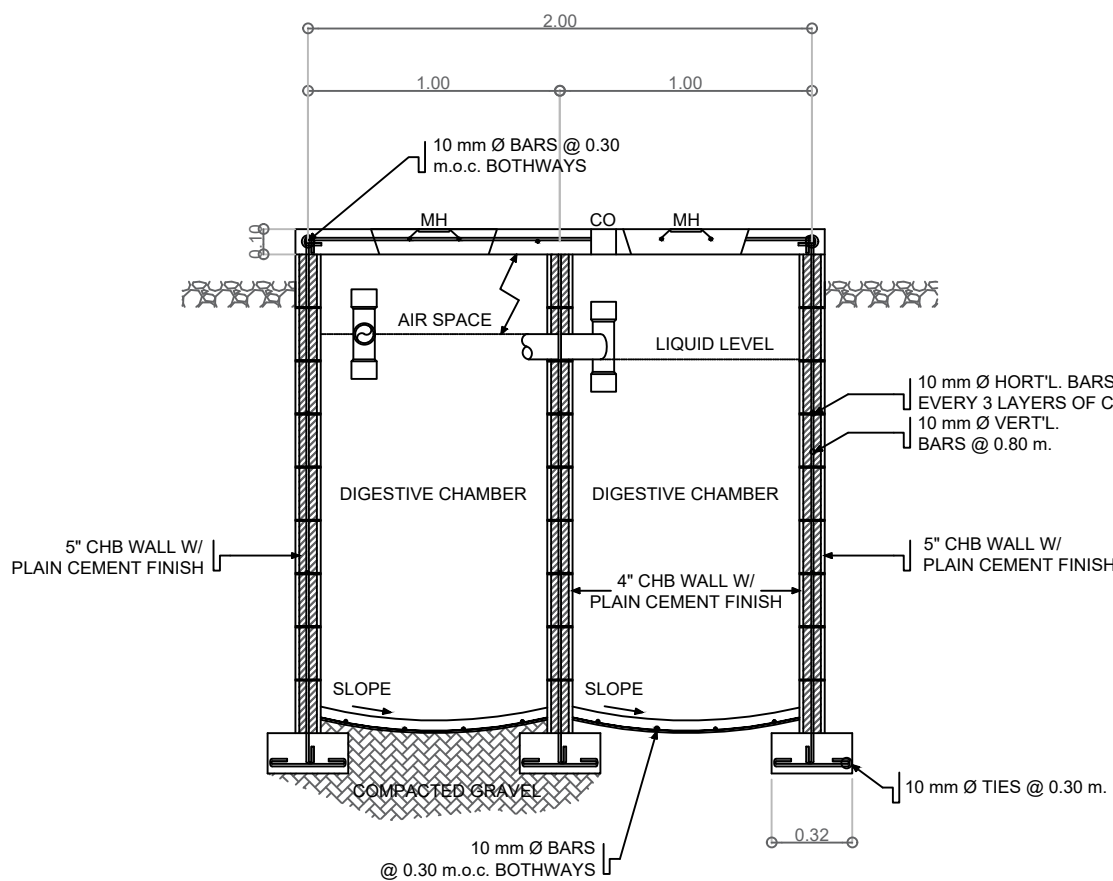

SECTION


3 SEPTIC VAULT DETAILS
P1 P1 SCALE 1 : 30 M.

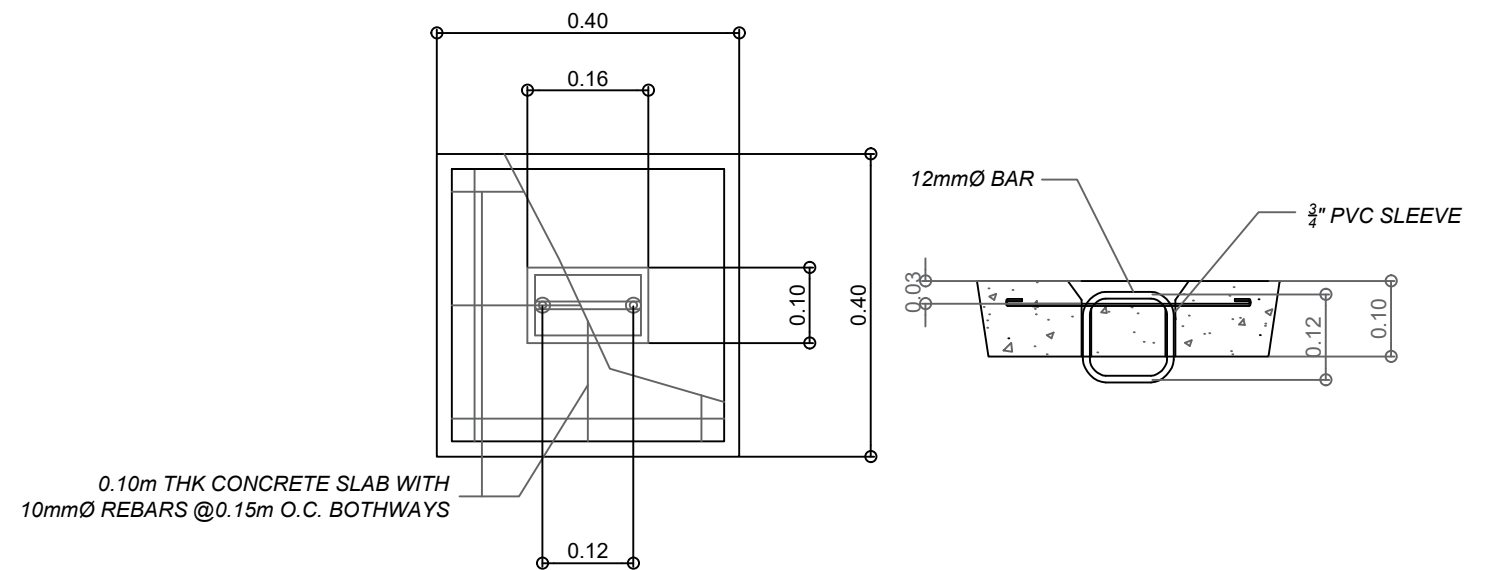

PLAN

SECTION

4 MANHOLE DETAILS
P1 P1 SCALE 1 : 10 M.

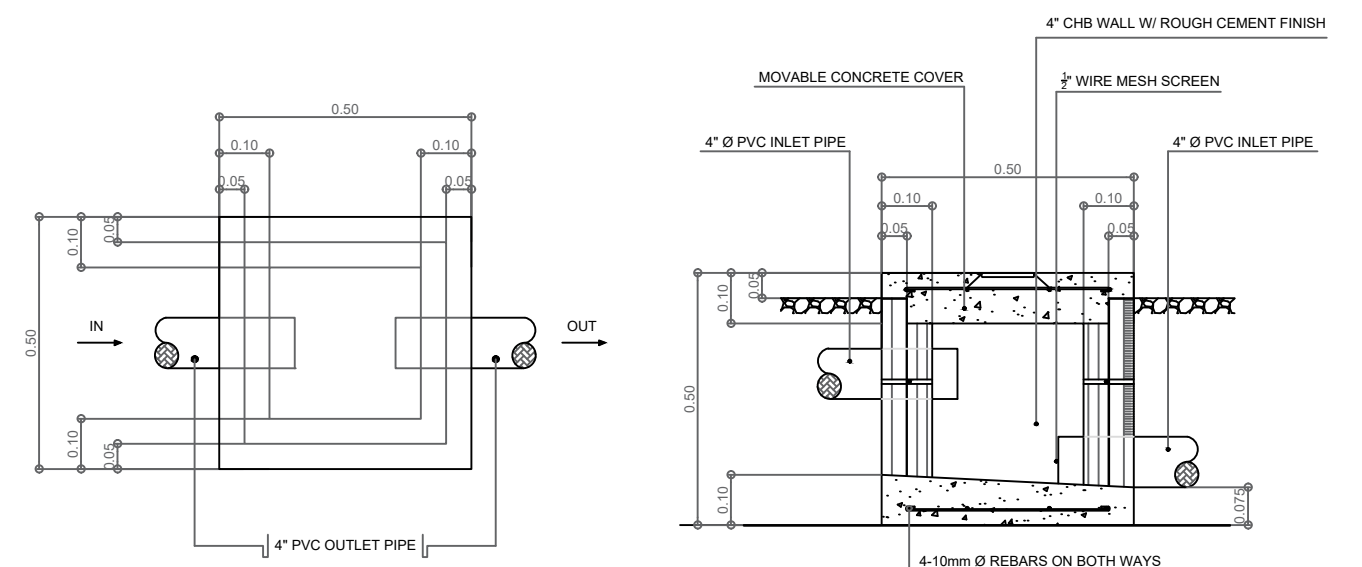


PLAN

SECTION


5 CATCH BASIN DETAILS
P1 P1 SCALE 1 : 15 M.

PLUMBING NOTES:

- ALL WORKS SHALL BE DONE UNDER THE DIRECT SUPERVISION OF A LICENSED
- INSTALL ALL FIXTURES & ACCESSORIES IN LOCATION DIRECTED IN ACCORDANCE W/ MANUFACTURER INSTRUCTIONS, MINIMIZING PIPE FITTINGS.
- ALL GI PIPES, PVC PIPES, & DRAINAGE PIPES SHALL HAVE A MINIMUM SLOPE OF 1%.
- FIXTURES AND ACCESSORIES MUST BE STANDARD OR EQUIVALENT.
- ALL CHANGES ON PIPE SIZES ON SOIL, WASTE, DRAIN LINE SHALL BE PROVIDED W/ REDUCING FITTING OR RECESSES REDUCER.
- CLEATS, PLATES, & ANCHOR REQUIRED TO SUPPORT FIXTURE RIGIDLY PLACE.
- INSTALL PLUMBING FIXTURES FREE& OPEN TO AFFORD EASY ACCESS FOR CLEANING.
- PROTECT ITEMS W/ APPROVAL MEANS TO MAINTAIN PERFECT W/O EXTRA COST TO THE OWNER.
- PROVIDE CORRECTLY LOCATED OPENING OF PROPER SIZES WHERE REQUIRED, IN WALLS AND FLOORS FOR PASSAGE PIPES.
- ALL PIPES SHALL BE CUT ACCURATELY TO MEASUREMENTS & WORKED INTO PLACE W/O SPRINGING OR FORCE
- CARE SHALL BE TAKEN AS NOT TO WEAKEN STRUCTURAL PORTION OF THE BUILDING.

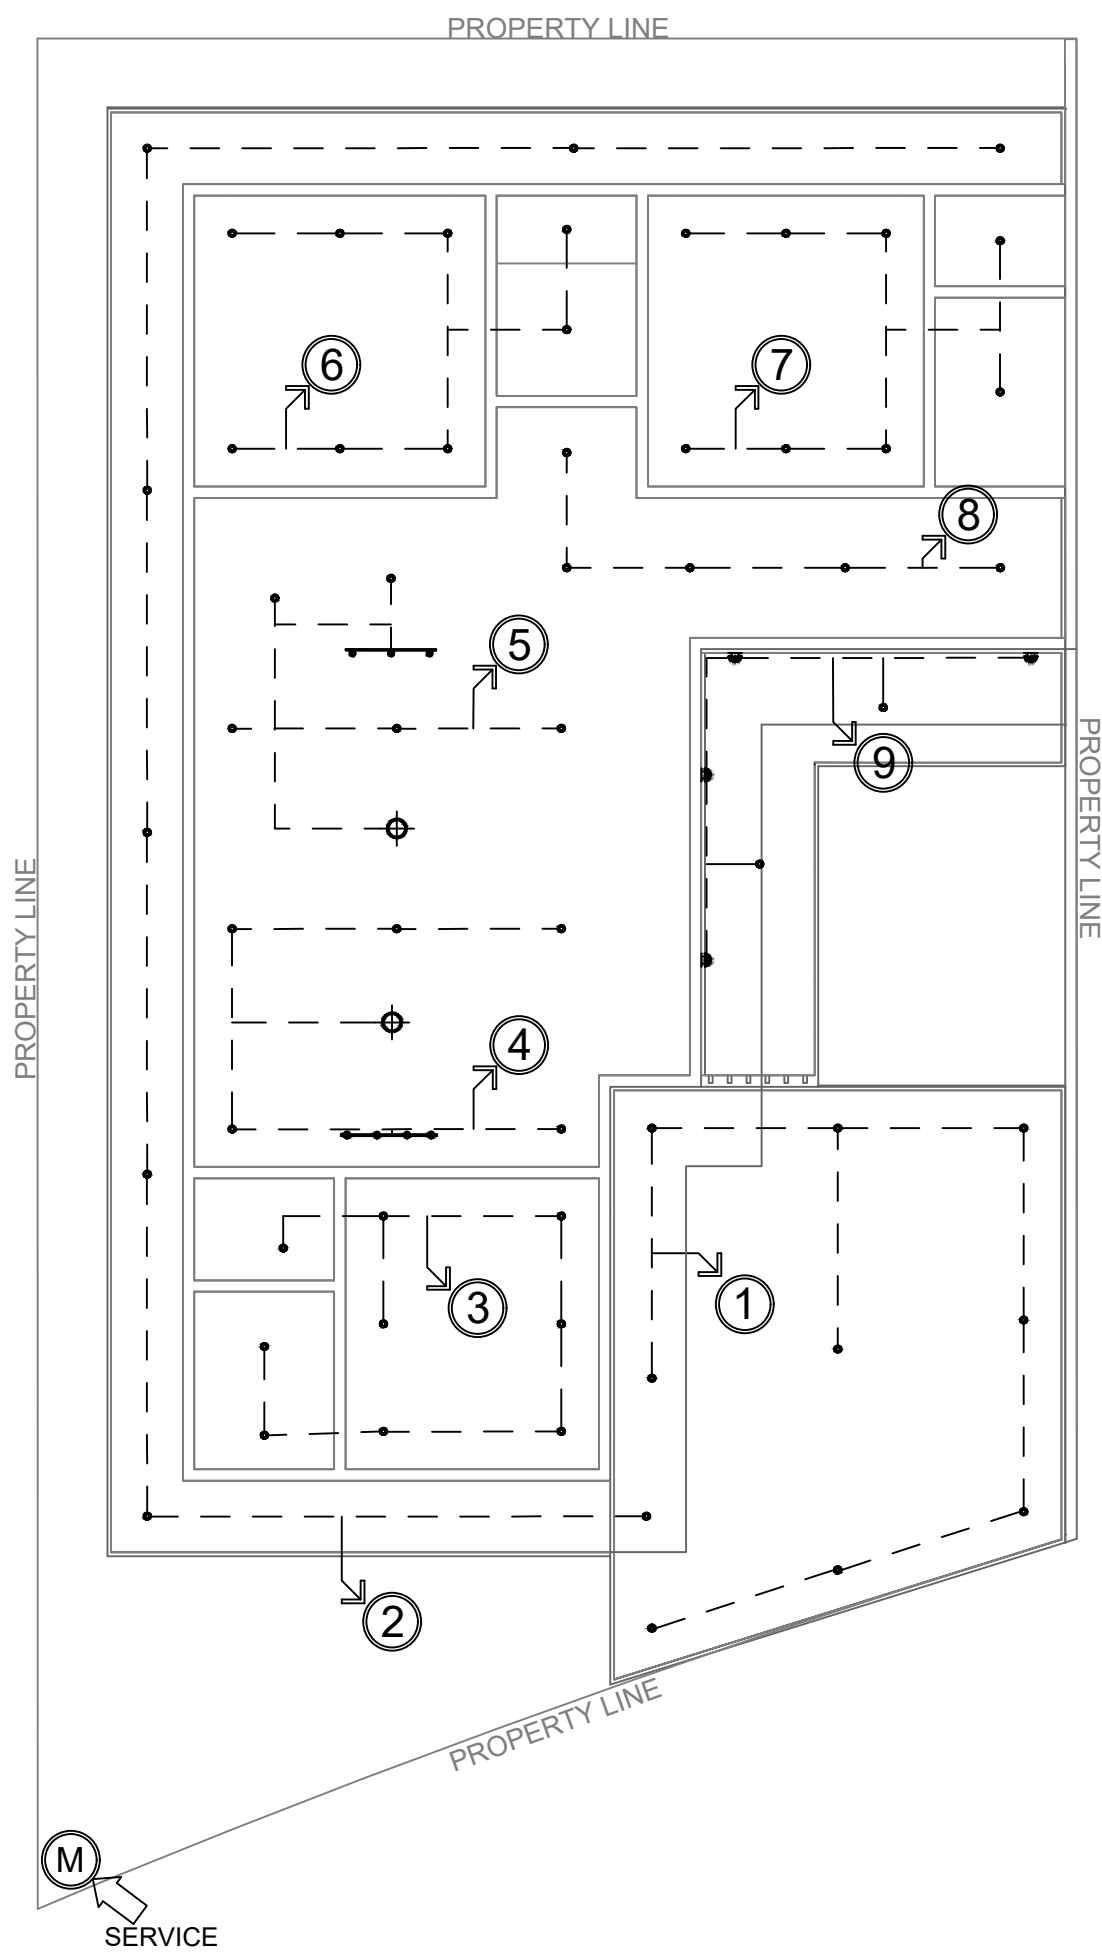

1 LIGHTING LAYOUT
E1 E1 SCALE 1 : 100 M.

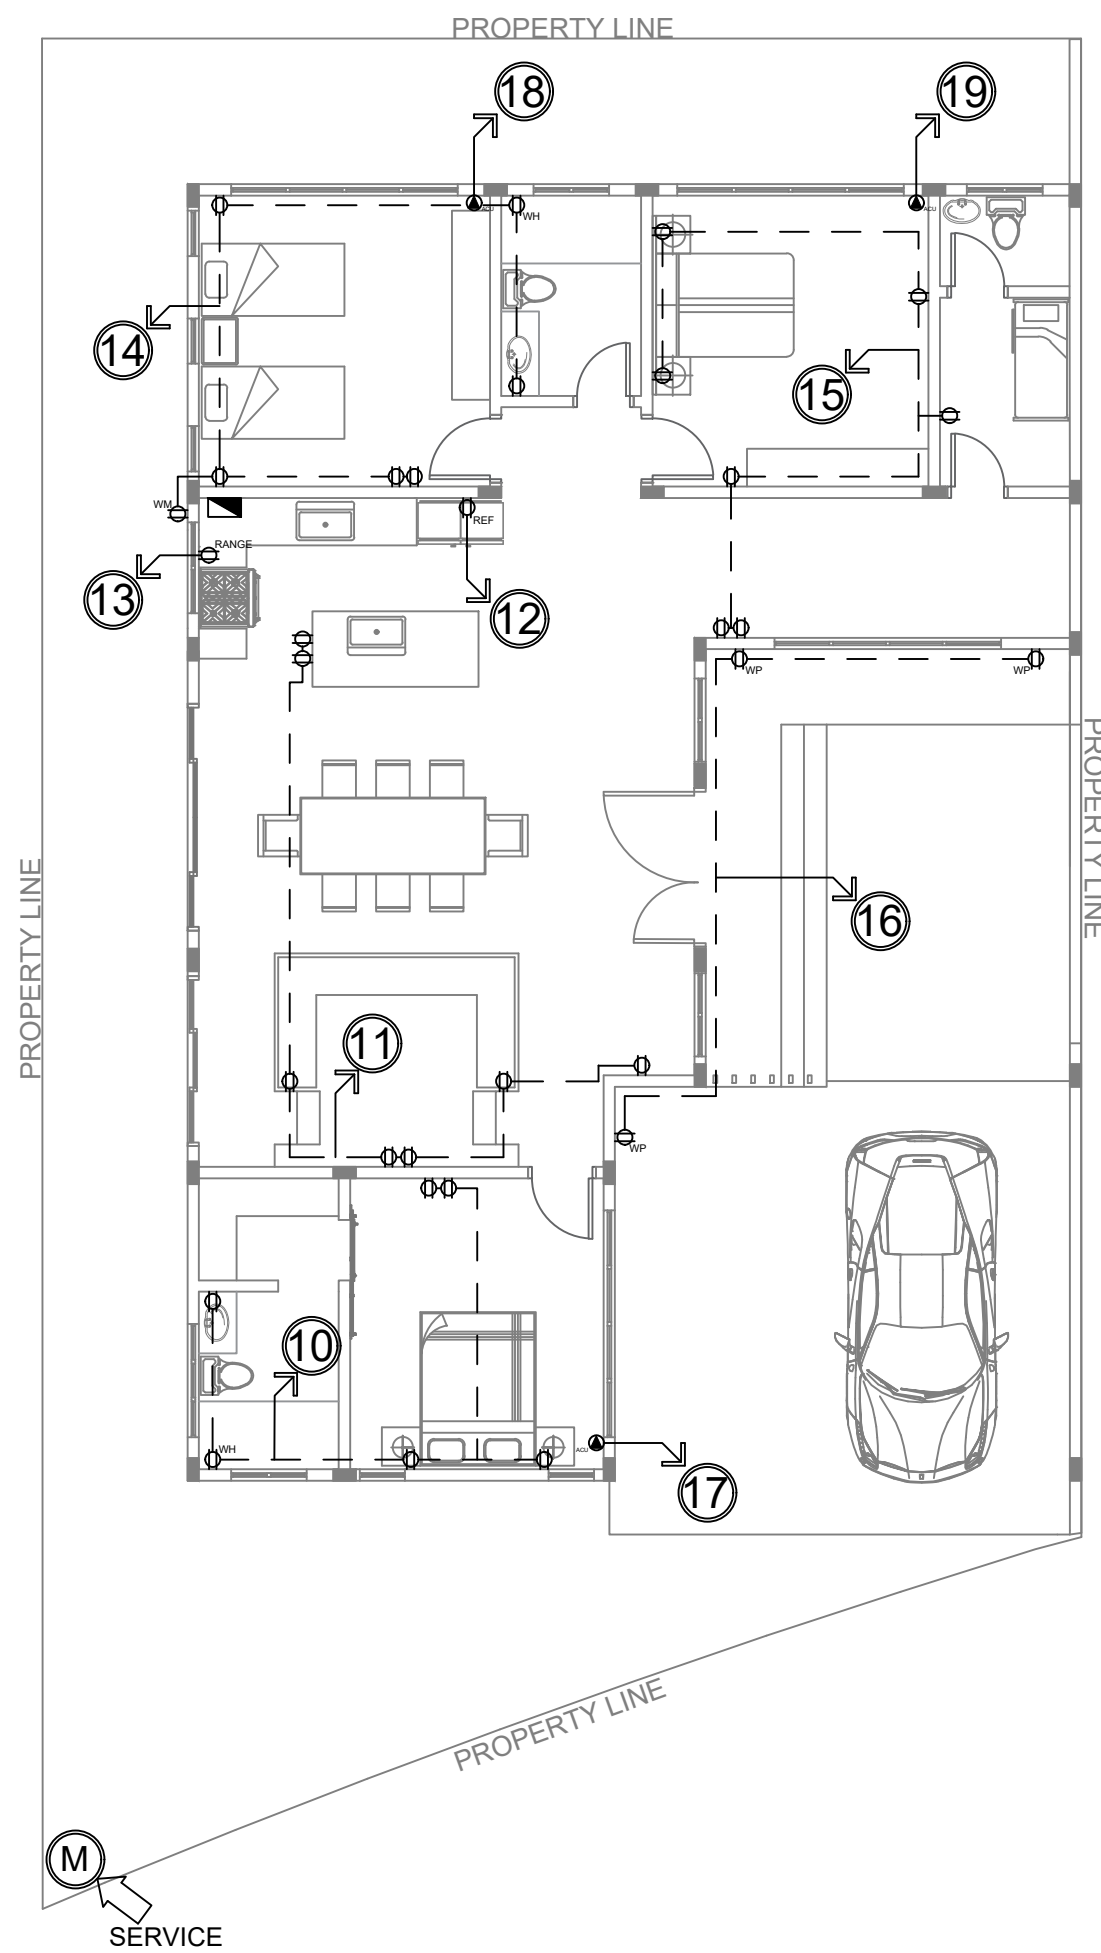

2 POWER LAYOUT
E1 E1 SCALE 1 : 100 M.

MOUNTING HEIGHTS

A. PANEL BOARD	1.80 M.
B. SWITCHES	1.40 M.
C. CONVENIENCE OUTLET	0.30 M.
D. CONVENIENCE OUTLET - *	1.00 M.
E. CATV / TEL.	0.30 M.
F. RANGE / REF	1.00 M.
G. KILOWATTHR. METER	1.80 M.
H. WATER HEATER	1.80 M.
I. INTERCOM	1.40 M.
J. AIR CONDITION UNIT	1.60 M.


ELECTRICAL SYMBOLS

	INCANDESCENT / PL LIGHT		TELEPHONE OUTLET
	PINLIGHT		CATV OUTLET
	FLUORESCENT LAMP		EXHAUST FAN
	WALL LAMP		CIRCUIT HOMERUN
	T5 LIGHTS (1.20M)		CIRCUIT NUMBER
	SWITCHES		GROUND
	DUPLEX CONVENIENCE OUTLET		CIRCUIT BREAKER
	DUPLEX CONVENIENCE OUTLET		PANEL BOARD
	WASHING MACHINE OUTLET		ELECTRIC METER
	AIR CONDITION UNIT OUTLET		SERVICE ENTRANCE

LOAD SCHEDULE											LOCATION: STORAGE	
CKT. NO.	LOAD SCHEDULE	LOCATION	VOLTS	AMPS	VOLT AMPS	CIRCUIT BREAKER				SIZE OF WIRE AND CONDUIT (sq.mm)	MMØ	
						POLE	AF	AT	KAIC		SIZE	TYPE
1	9 - PINLIGHT	CARPORT	230	0.98	225	2	50	20	10	2 - 3.5 mm ² THHN WIRE 1 - 2.0 mm ² THHN WIRE	20	PVC
2	8 - PINLIGHT	LANAI	230	0.87	200	2	50	20	10	- do -	20	PVC
3	9 - PINLIGHT	MASTER'S BEDROOM	230	0.98	225	2	50	20	10	- do -	20	PVC
4	5 - PINLIGHT, 2 - LIGHTING OUTLET	LIVING ROOM	230	3.15	725	2	50	20	10	- do -	20	PVC
5	5 - PINLIGHT, 2 - LIGHTING OUTLET	DINING ROOM, KITCHEN	230	3.15	725	2	50	20	10	- do -	20	PVC
6	8 - PINLIGHT	BEDROOM 1, T&B	230	0.87	200	2	50	20	10	- do -	20	PVC
7	8 - PINLIGHT	BEDROOM 2, MAID'S ROOM	230	0.87	200	2	50	20	10	- do -	20	PVC
8	5 - PINLIGHT	HALLWAY	230	0.54	125	2	50	20	10	- do -	20	PVC
9	6 - PINLIGHT	PORCH	230	0.65	150	2	50	20	10	- do -	20	PVC
10	6 - CONVENIENCE OUTLET	MASTER'S BEDROOM & T&B	230	4.70	1080	2	50	20	10	- do -	20	PVC
11	7 - CONVENIENCE OUTLET	LIVING ROOM, KITCHEN	230	5.48	1260	2	50	20	10	- do -	20	PVC
12	1 - REF OUTLET	KITCHEN	230	13.04	3000	2	50	30	10	2 - 5.5 mm ² THHN WIRE 1 - 2.0 mm ² THHN WIRE	20	PVC
13	1 - RANGE OUTLET	KITCHEN	230	13.04	3000	2	50	30	10	- do -	20	PVC
14	7 - CONVENIENCE OUTLET	BEDROOM 1	230	5.48	1260	2	50	20	10	2 - 3.5 mm ² THHN WIRE 1 - 2.0 mm ² THHN WIRE	20	PVC
15	7 - CONVENIENCE OUTLET	BEDROOM 2, MAID'S ROOM, HALLWAY	230	5.48	1260	2	50	20	10	- do -	20	PVC
16	3 - CONVENIENCE OUTLET	PORCH, CARPORT	230	2.35	540	2	50	20	10	- do -	20	PVC
17	1 - ACU OUTLET	MASTER'S BEDROOM	230	10	2300	2	50	30	10	2 - 5.5 mm ² THHN WIRE 1 - 2.0 mm ² THHN WIRE	20	PVC
18	1 - ACU OUTLET	BEDROOM 1	230	10	2300	2	50	30	10	- do -	20	PVC
19	1 - ACU OUTLET	BEDROOM 2	230	10	2300	2	50	30	10	- do -	20	PVC
20	SPARE	-	230	-	-	2	50	20	10	2 - 3.5 mm ² THHN WIRE 1 - 2.0 mm ² THHN WIRE	20	PVC
21	SPARE	-	230	-	-	2	50	20	10	- do -	20	PVC
22	SPARE	-	230	-	-	2	50	20	10	- do -	20	PVC
TOTAL CONNECTED LOAD			230	91.63	21075					2 - 30 mm ² THHN WIRE 1 - 14 mm ² TW WIRE	40	PVC

GENERAL NOTES AND SPECIFICATIONS

- ALL WORK SHALL BE DONE IN ACCORDANCE WITH THE PLANS AND SPECIFICATIONS.
- THE WORK SHALL COMPLY WITH THE PROVISION OF THE LATEST EDITION OF THE PHILIPPINE ELECTRICAL CODE OF LAWS, ORDINANCES RULES AND REGULATIONS OF THE LOCALITY HAVING THE JURISDICTION OVER THE PROJECT AND THE REQUIREMENT OF THE UTILITY COMPANY.
- THE JOB SHALL BE DONE IN THE MOST THOROUGH PROMPT AND WORKMAN LIKE MANNER UTILIZING STANDARD TOLLS. EQUIPMENT, METHODS, AND GOOD ENGINEERING PRACTICE, THE JOB SHALL BE DONE COMPLETE IN ALL ASPECT OF REQUIRED PER PLANS, SPECIFICATIONS AND READY FOR OPERATION.
- ALL MATERIALS TO BE USED SHALL BE OF BEST QUALITY AND BRAND NEW AS SPECIFIED.
- ALL CONDUIT SHALL BE CONCEALED INSIDE THE CEILING, FLOOR AND WALLS.
- USE ADEQUATE GROUNDING SYSTEM AND PROVIDE IF NECESSARY ADDITIONAL GROUND RODS TO MEET THE REQUIRED GROUND RESISTANCE.
- ALL CONDUIT SHALL BE PROTECTED AGAINST DAMAGES BY THE ENTRANCE OF WATER AND FOREIGN MATERIALS DURING CONSTRUCTION AND ALL OF CONDUITS SHALL BE PLEDGE TO EXCLUDE MOISTURE AND DUST IMMEDIATELY AFTER THE CONDUITS ARE PLACED.
- AIR CONDITIONING OUTLET, WATER HEATER, RANGE, REF SHALL BE RATED 300 VOLTS AND GROUNDING TYPE 230 VOLTS, 3 WIRE SYSTEM.

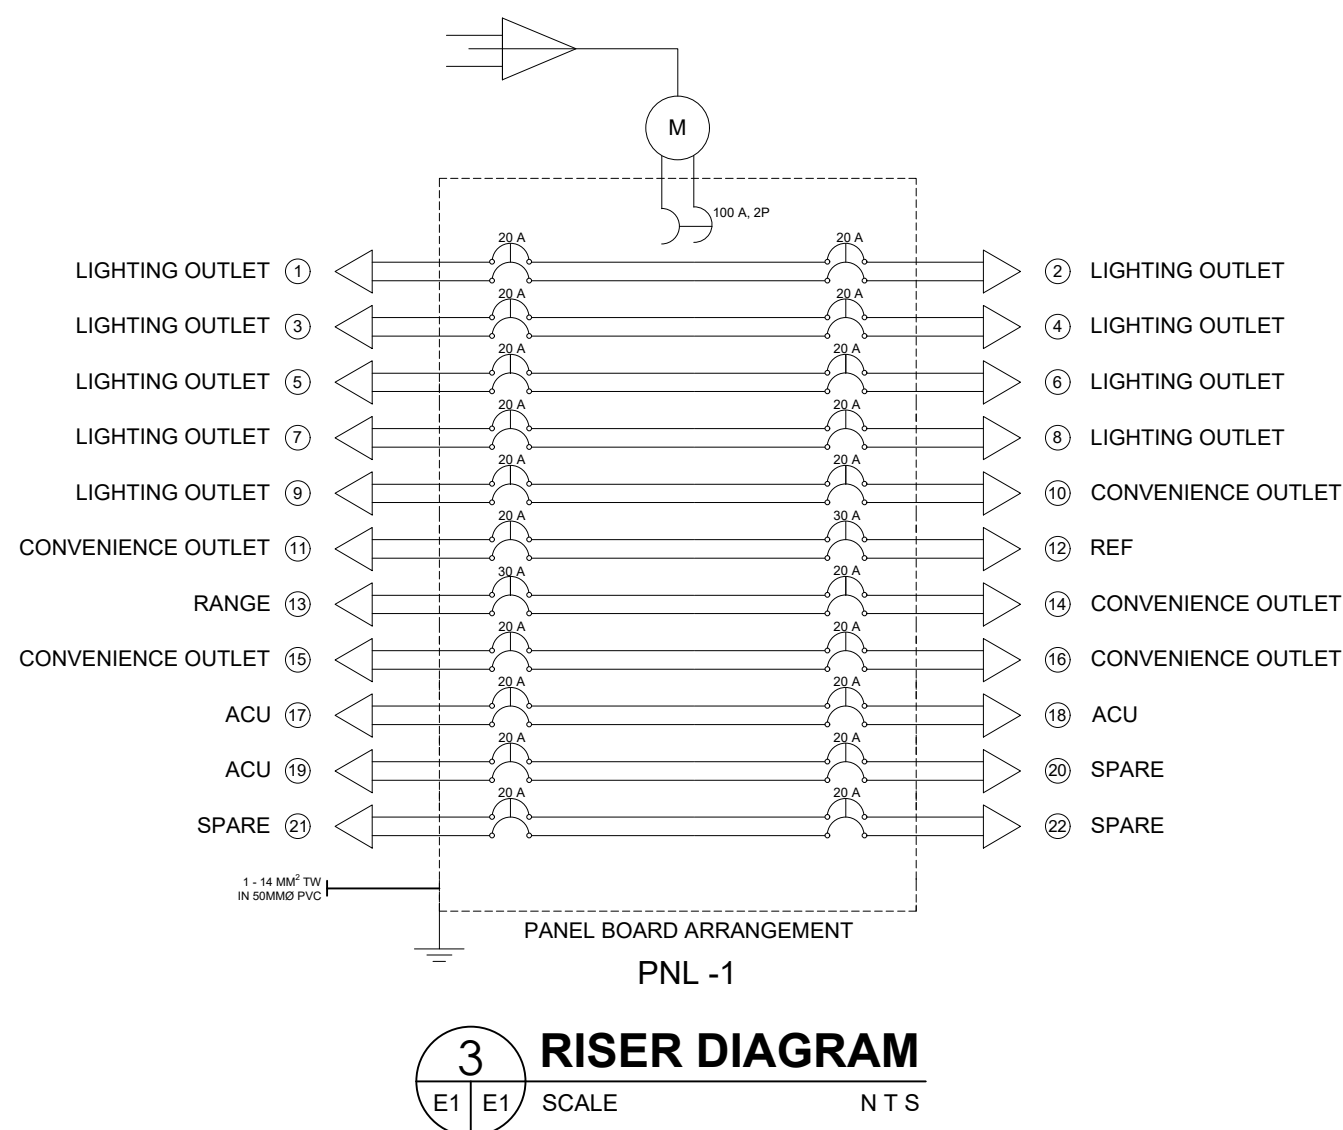

ARCHITECT		ENGINEER		RA 9266 (ARCHITECTURE ACT OF 2004) - SECTION 33	PROJECT / LOCATION	OWNER	DESIGNED:	No.	REVISIONS	DATE	SHEET CONTENT		SHEET No.	
				DRAWING & SPECIFICATION DULY SIGNED, STAMPED OR SEALED AS INSTRUMENT OF SERVICE ARE THE PROPERTY AND DOCUMENTS OF THE ARCHITECT. WHETHER THE OBJECT FOR WHICH THEY ARE MADE IS EXECUTED OR NOT, IT SHALL BE UNLAWFUL FOR ANY PERSON WITHOUT THE WRITTEN CONSENT OF THE ARCHITECT OR AUTHOR OF THE SAID DOCUMENTS TO DUPLICATE FOR USE IN THE REPETITION & FOR OTHER PROJECTS OR BUILDERS WETHER EXECUTED PARTLY OR IN WHOLE.	PROPOSED ONE STOREY RESIDENTIAL BUILDING	██								